

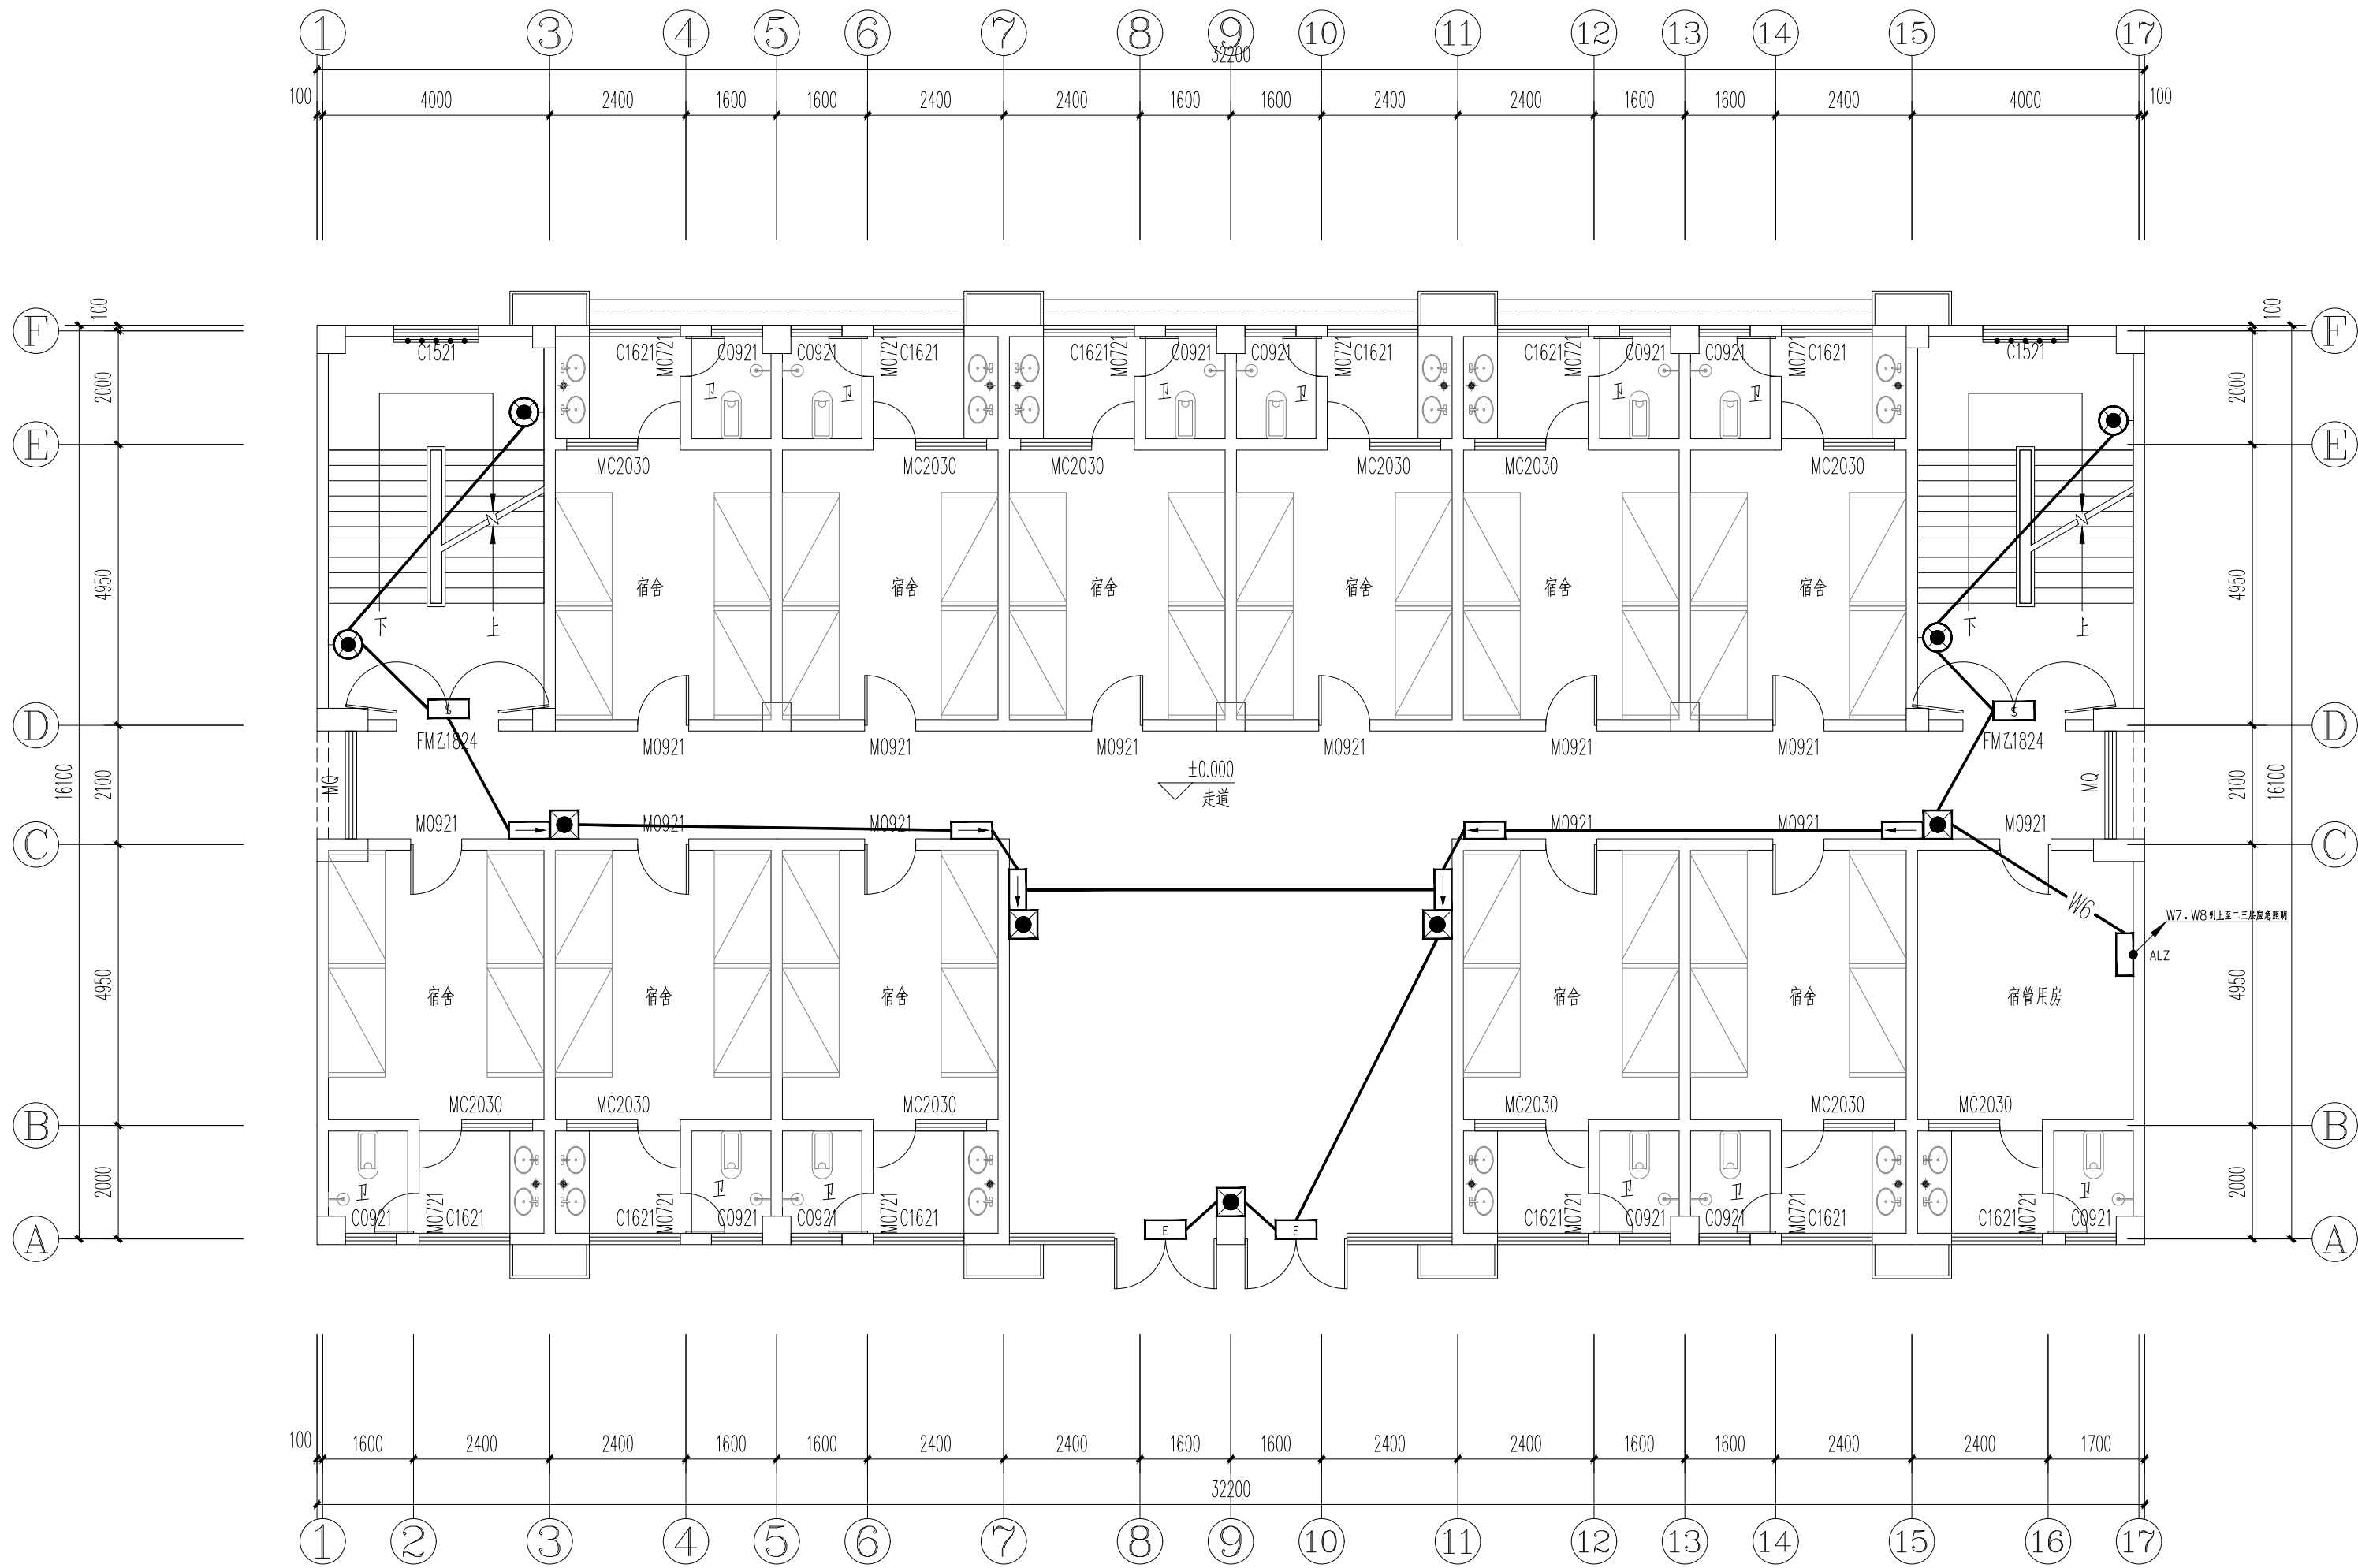


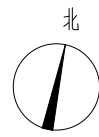

一层平面图 1:100

审定 Examined & Approved by		
审核 Examined & Verified by		
项目经理 Project Manager		
项目执行经理 Project implementation manager		
校核 Checked by		
专业负责人 Discipline Director		
设计 Designed by	赵鼎臣	
会签: Confirmed by	版本号: Version No.	
建筑: ARCH	电气: ELEC	
结构: STRU	弱电: WEAK-ELEC	
给排水: WS&S	暖通: HVAC	
图别: STATUS	施工图	图号: DRAWING NO.
设计号: PROJECT NO.	42301618	日期: DATE
		2026.6

注：所有图纸以版本号数字最大者为最终版本并以此为准。

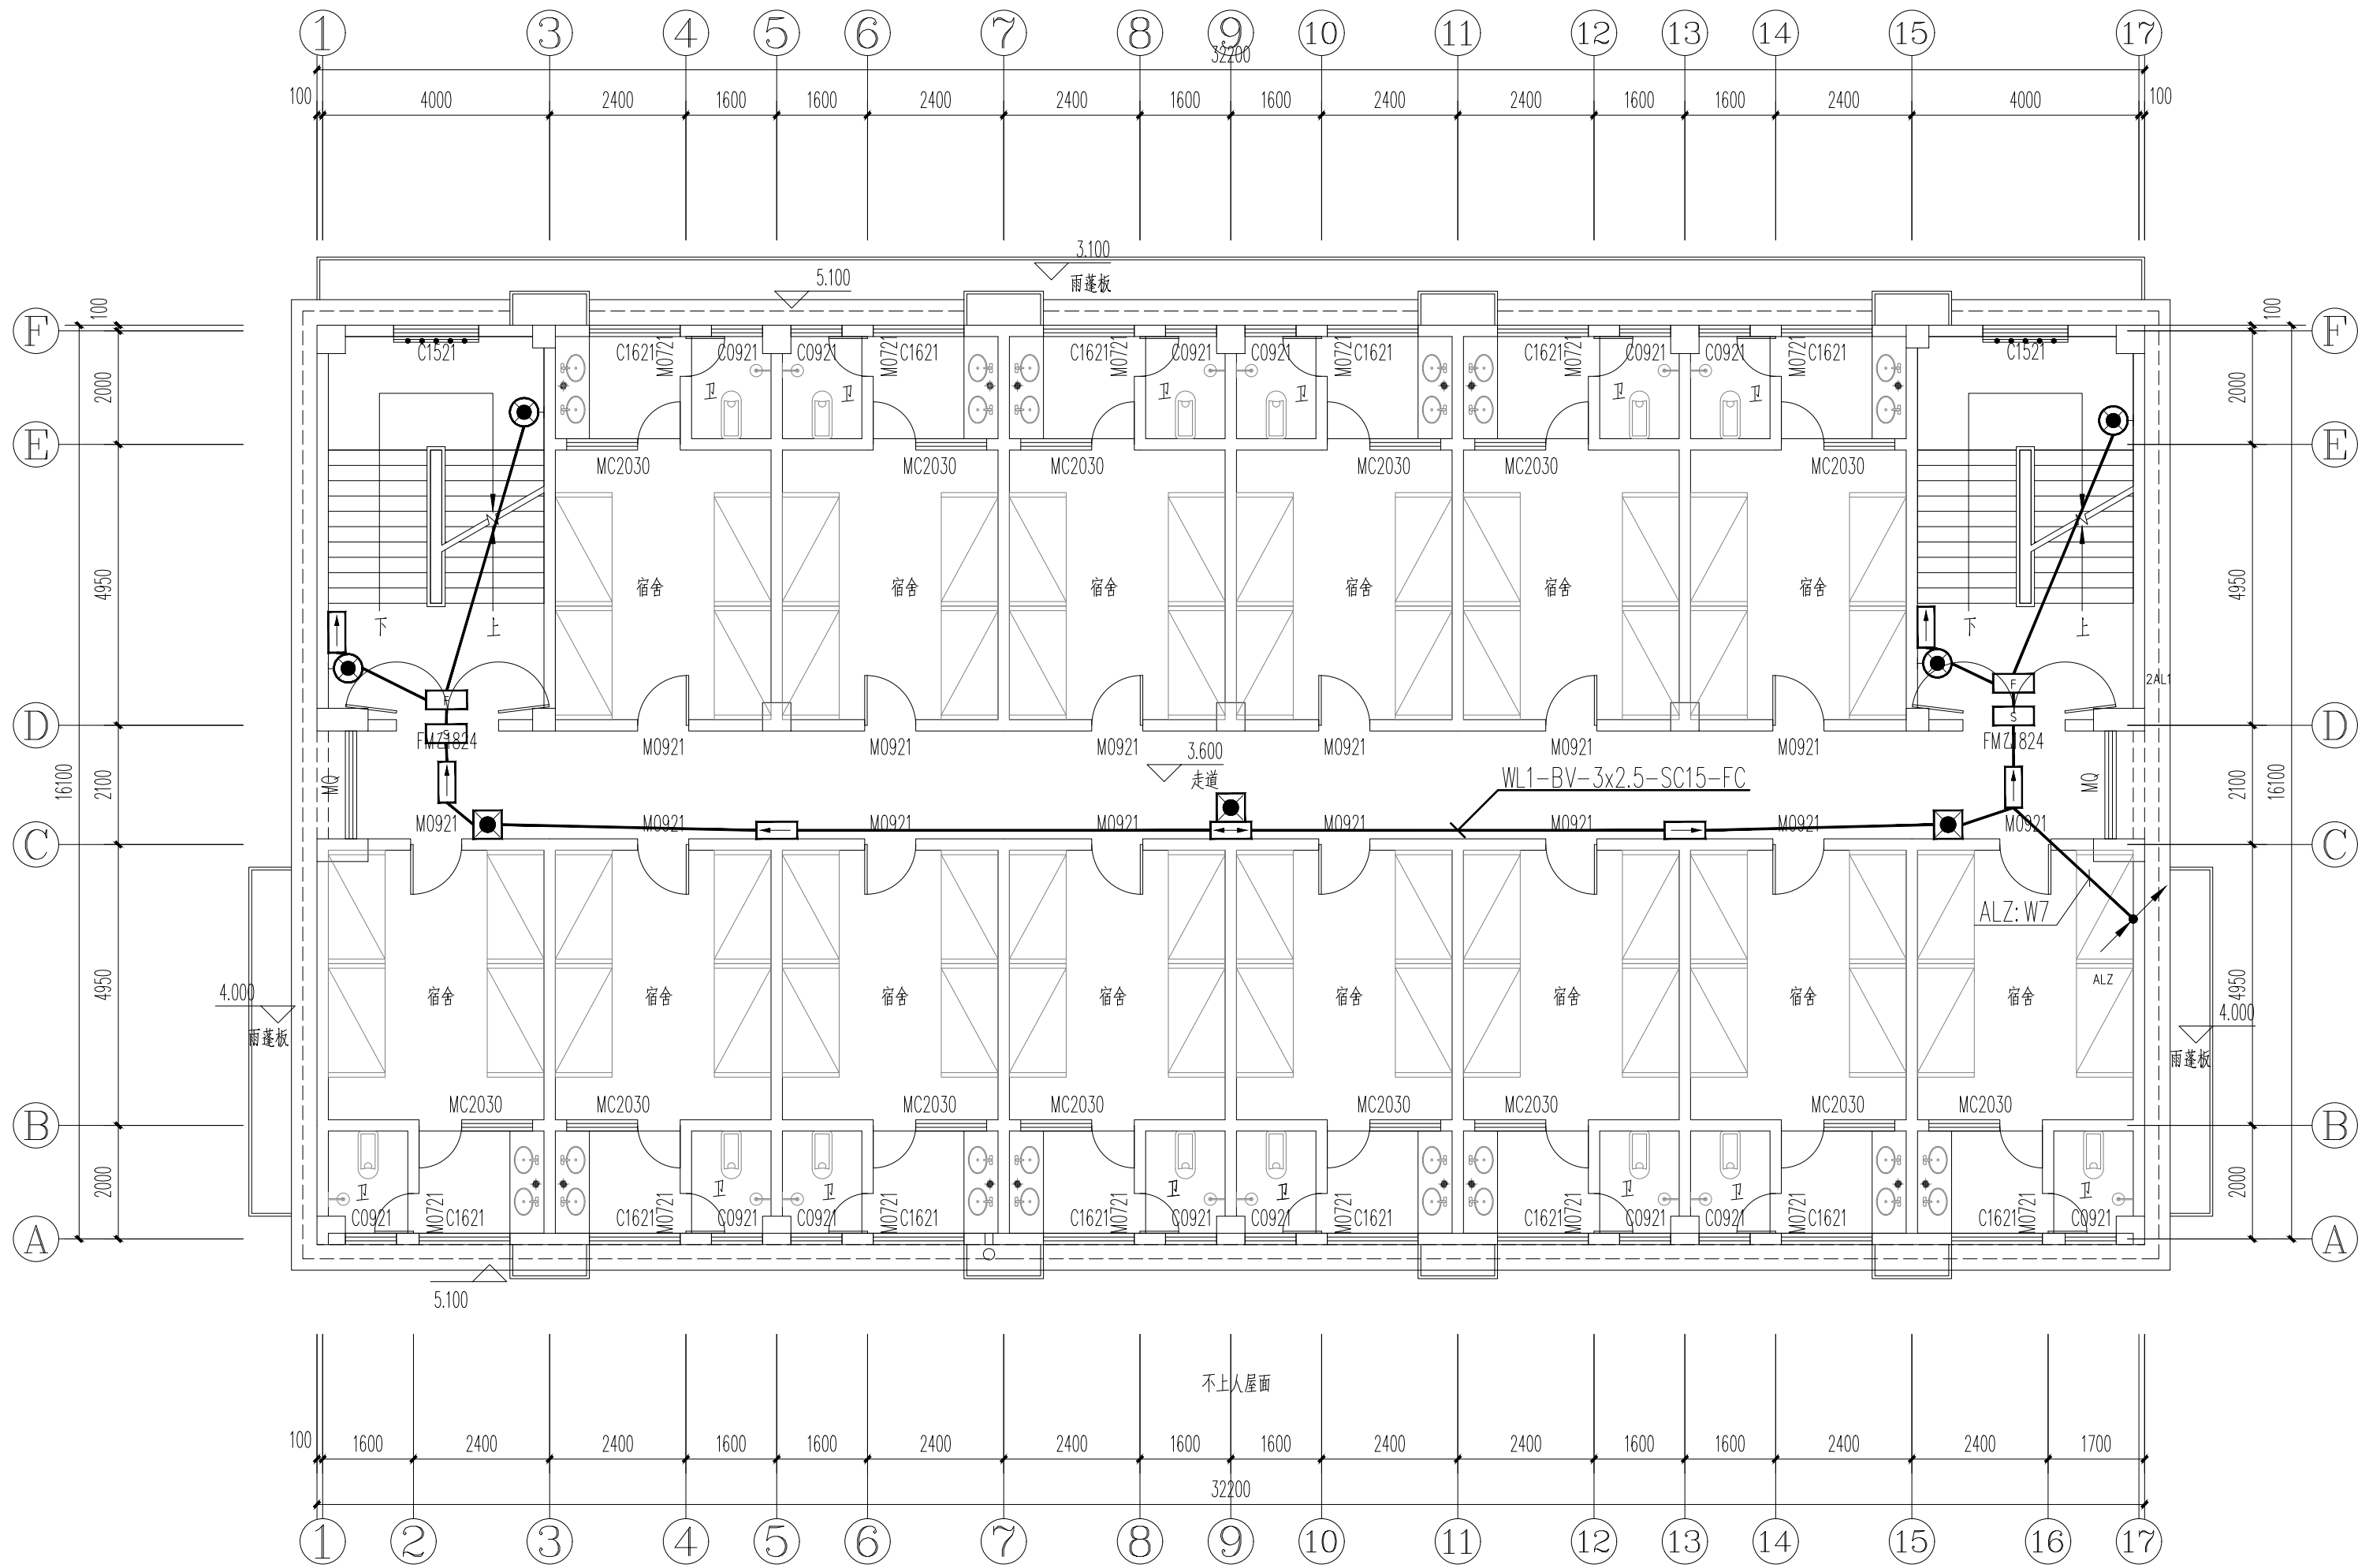

二层平面图 1:100



审定 Examined & Approved by		
审核 Examined & Verified by		
项目经理 Project Manager		
项目执行经理 Project implementation manager		
校核 Checked by		
专业负责人 Discipline Director		
设计 Designed by	赵胤臣	
会签: Confirmed by	版本号: Version No.	
建筑: ARCH	电气: ELEC	
结构: STRU	弱电: WEAK-ELEC	
给排水: WS&S	暖通: HVAC	
图别: STATUS	施工图	图号: DRAWING NO.
设计号: PROJECT NO.	42301618	日期: DATE
		2026.6

注：所有图纸以版本号数字最大者为最终版本并以此为准。



审定 Examined & Approved by			
审核 Examined & Verified by			
项目经理 Project Manager			
项目执行经理 Project Implementation manager			
校核 Checked by			
专业负责人 Discipline Director			
设计 Designed by	赵胤臣		
会签: Confirmed by		版本号: Version No.	
建筑: ARCH		电气: ELEC	
结构: STRU		弱电: WEAK-ELEC	
给排水: WSBS		暖通: HVAC	
图别: STATUS	施工图	图号: DRAWING NO.	1 / 15
设计号: PROJECT NO.	42301618	日期: DATE	2026.6


注：所有图纸以版本号数字最大者为最终版本并以此为准。

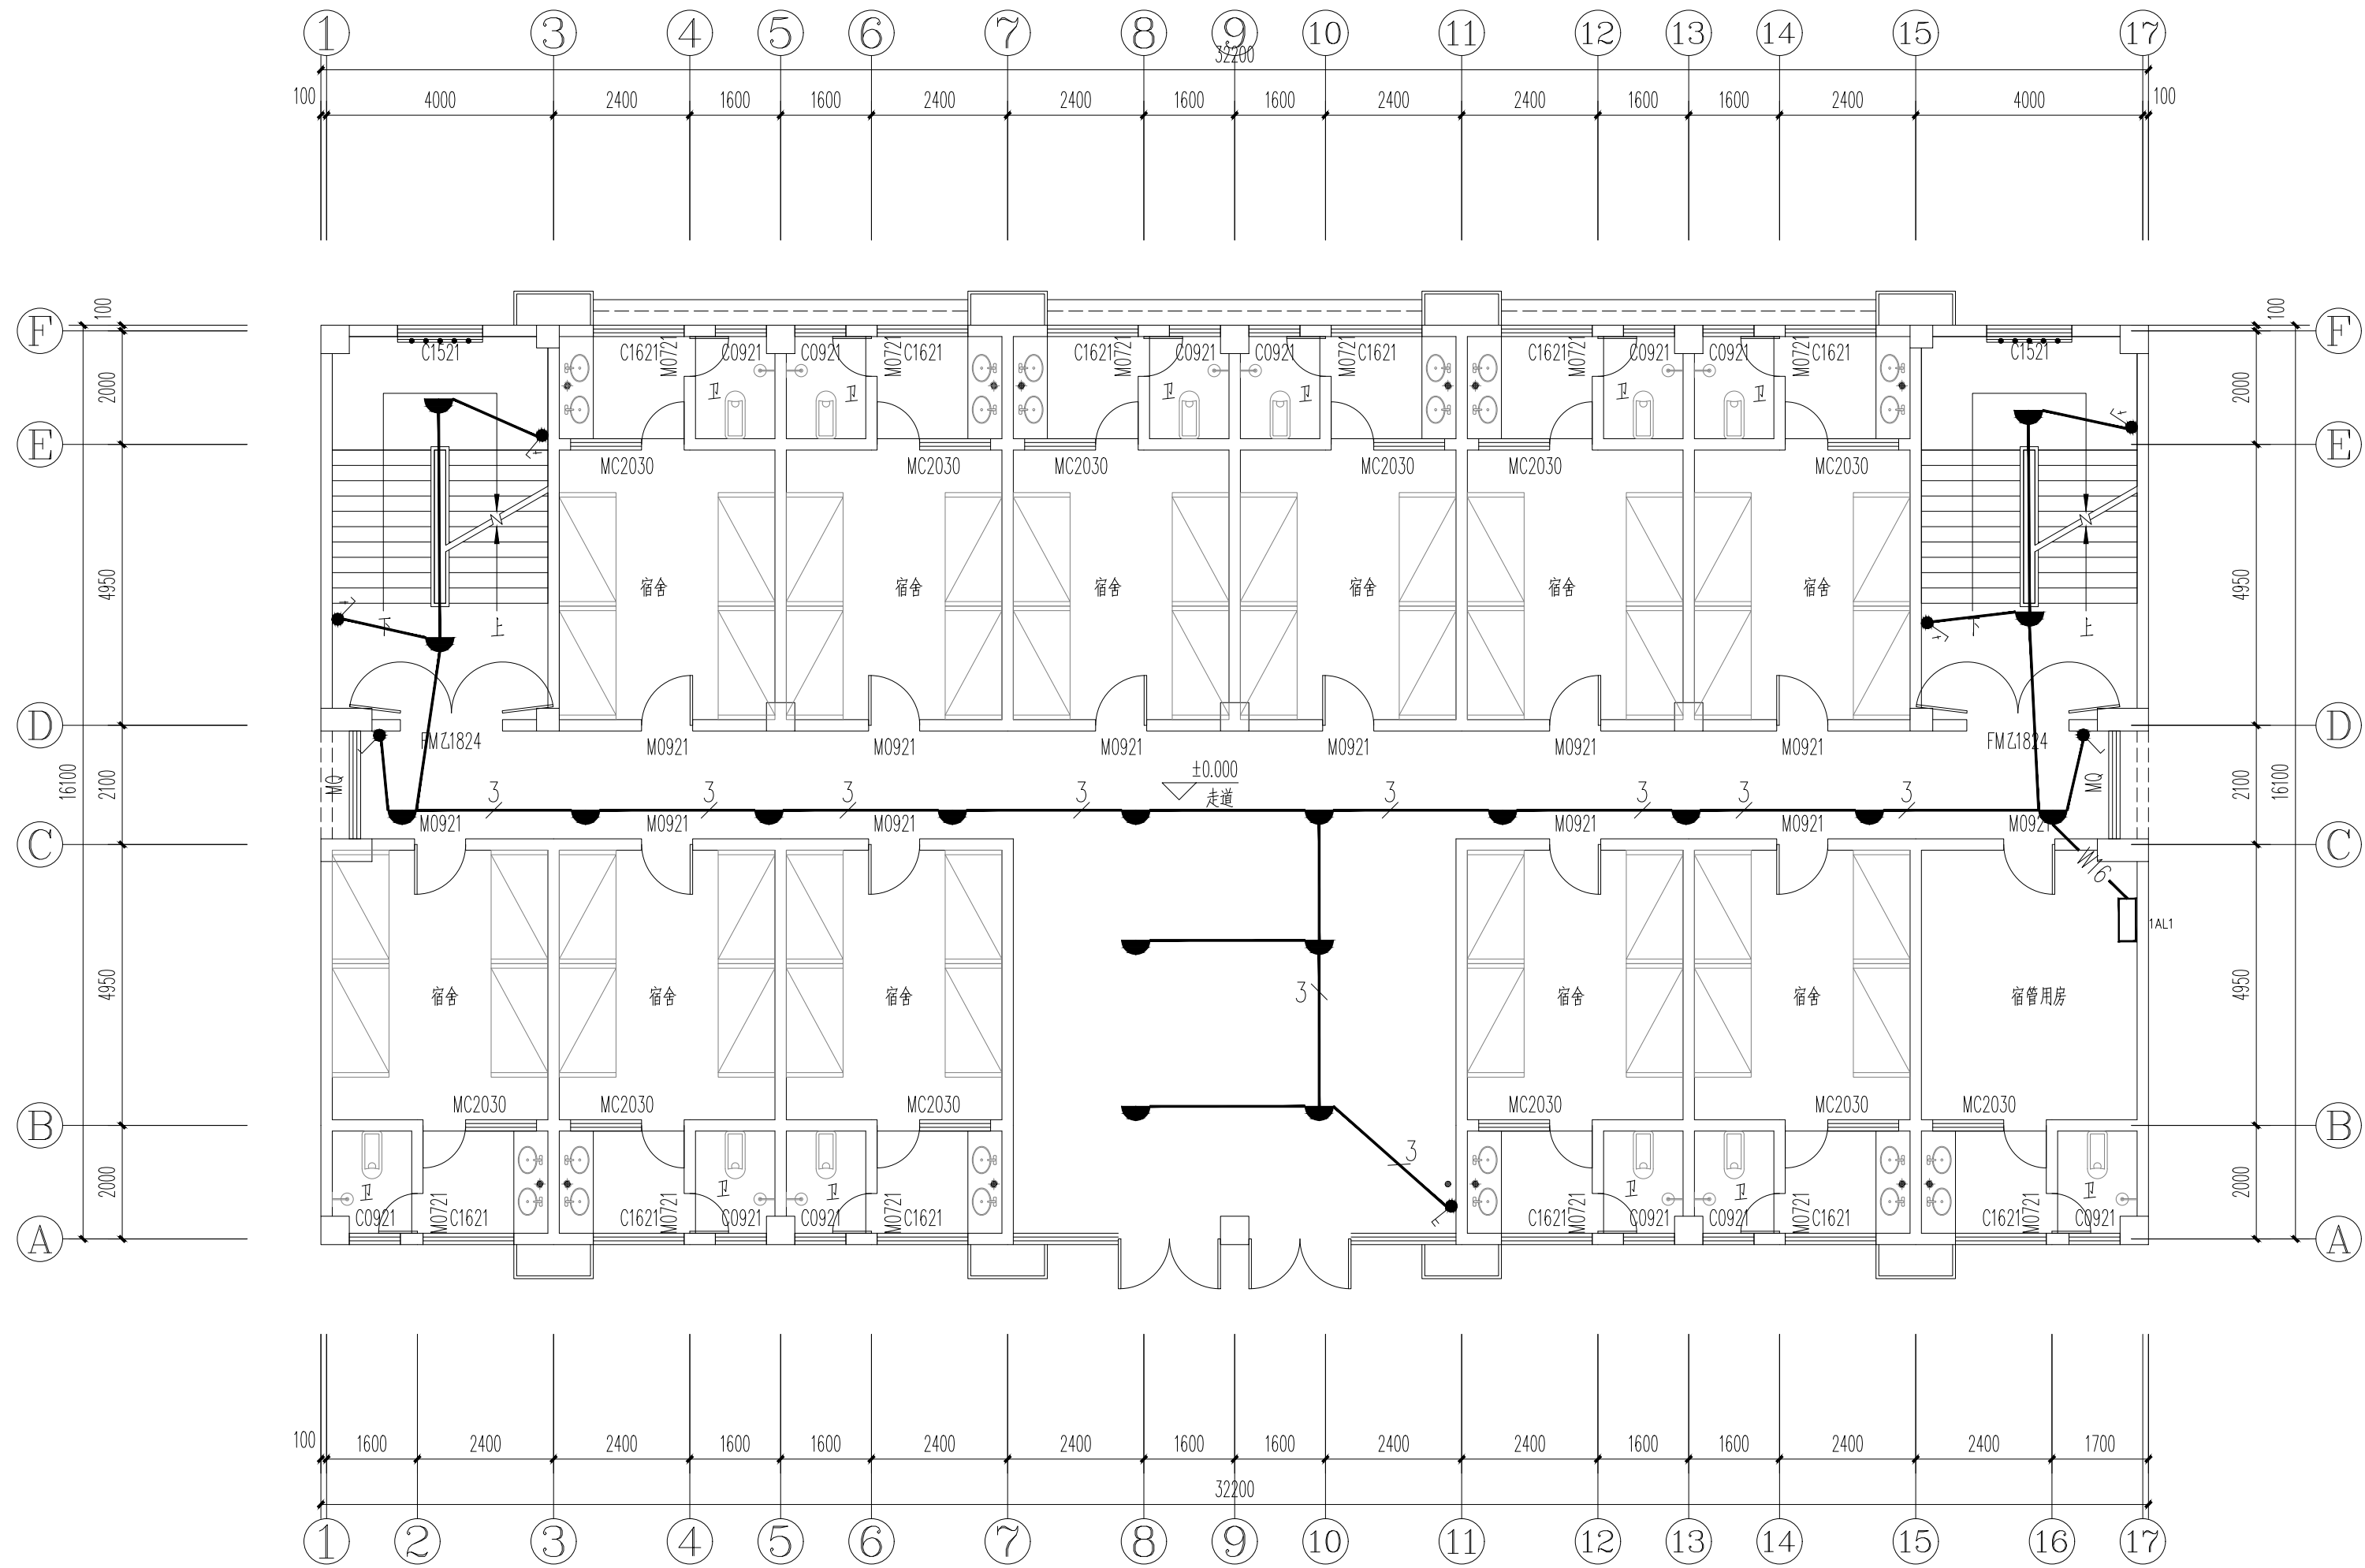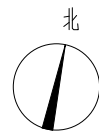

一层平面图 1:100

审定 Examined & Approved by		
审核 Examined & Verified by		
项目经理 Project Manager		
项目执行经理 Project implementation manager		
校核 Checked by		
专业负责人 Discipline Director		
设计 Designed by	赵鼎臣	
会签: Confirmed by	版本号: Version No.	
建筑: ARCH	电气: ELEC	
结构: STRU	弱电: WEAK-ELEC	
给排水: WS&S	暖通: HVAC	
图别: STATUS	施工图	图号: DRAWING NO.
设计号: PROJECT NO.	42301618	日期: DATE
		2026.6


注：所有图纸以版本号数字最大者为最终版本并以此为准。

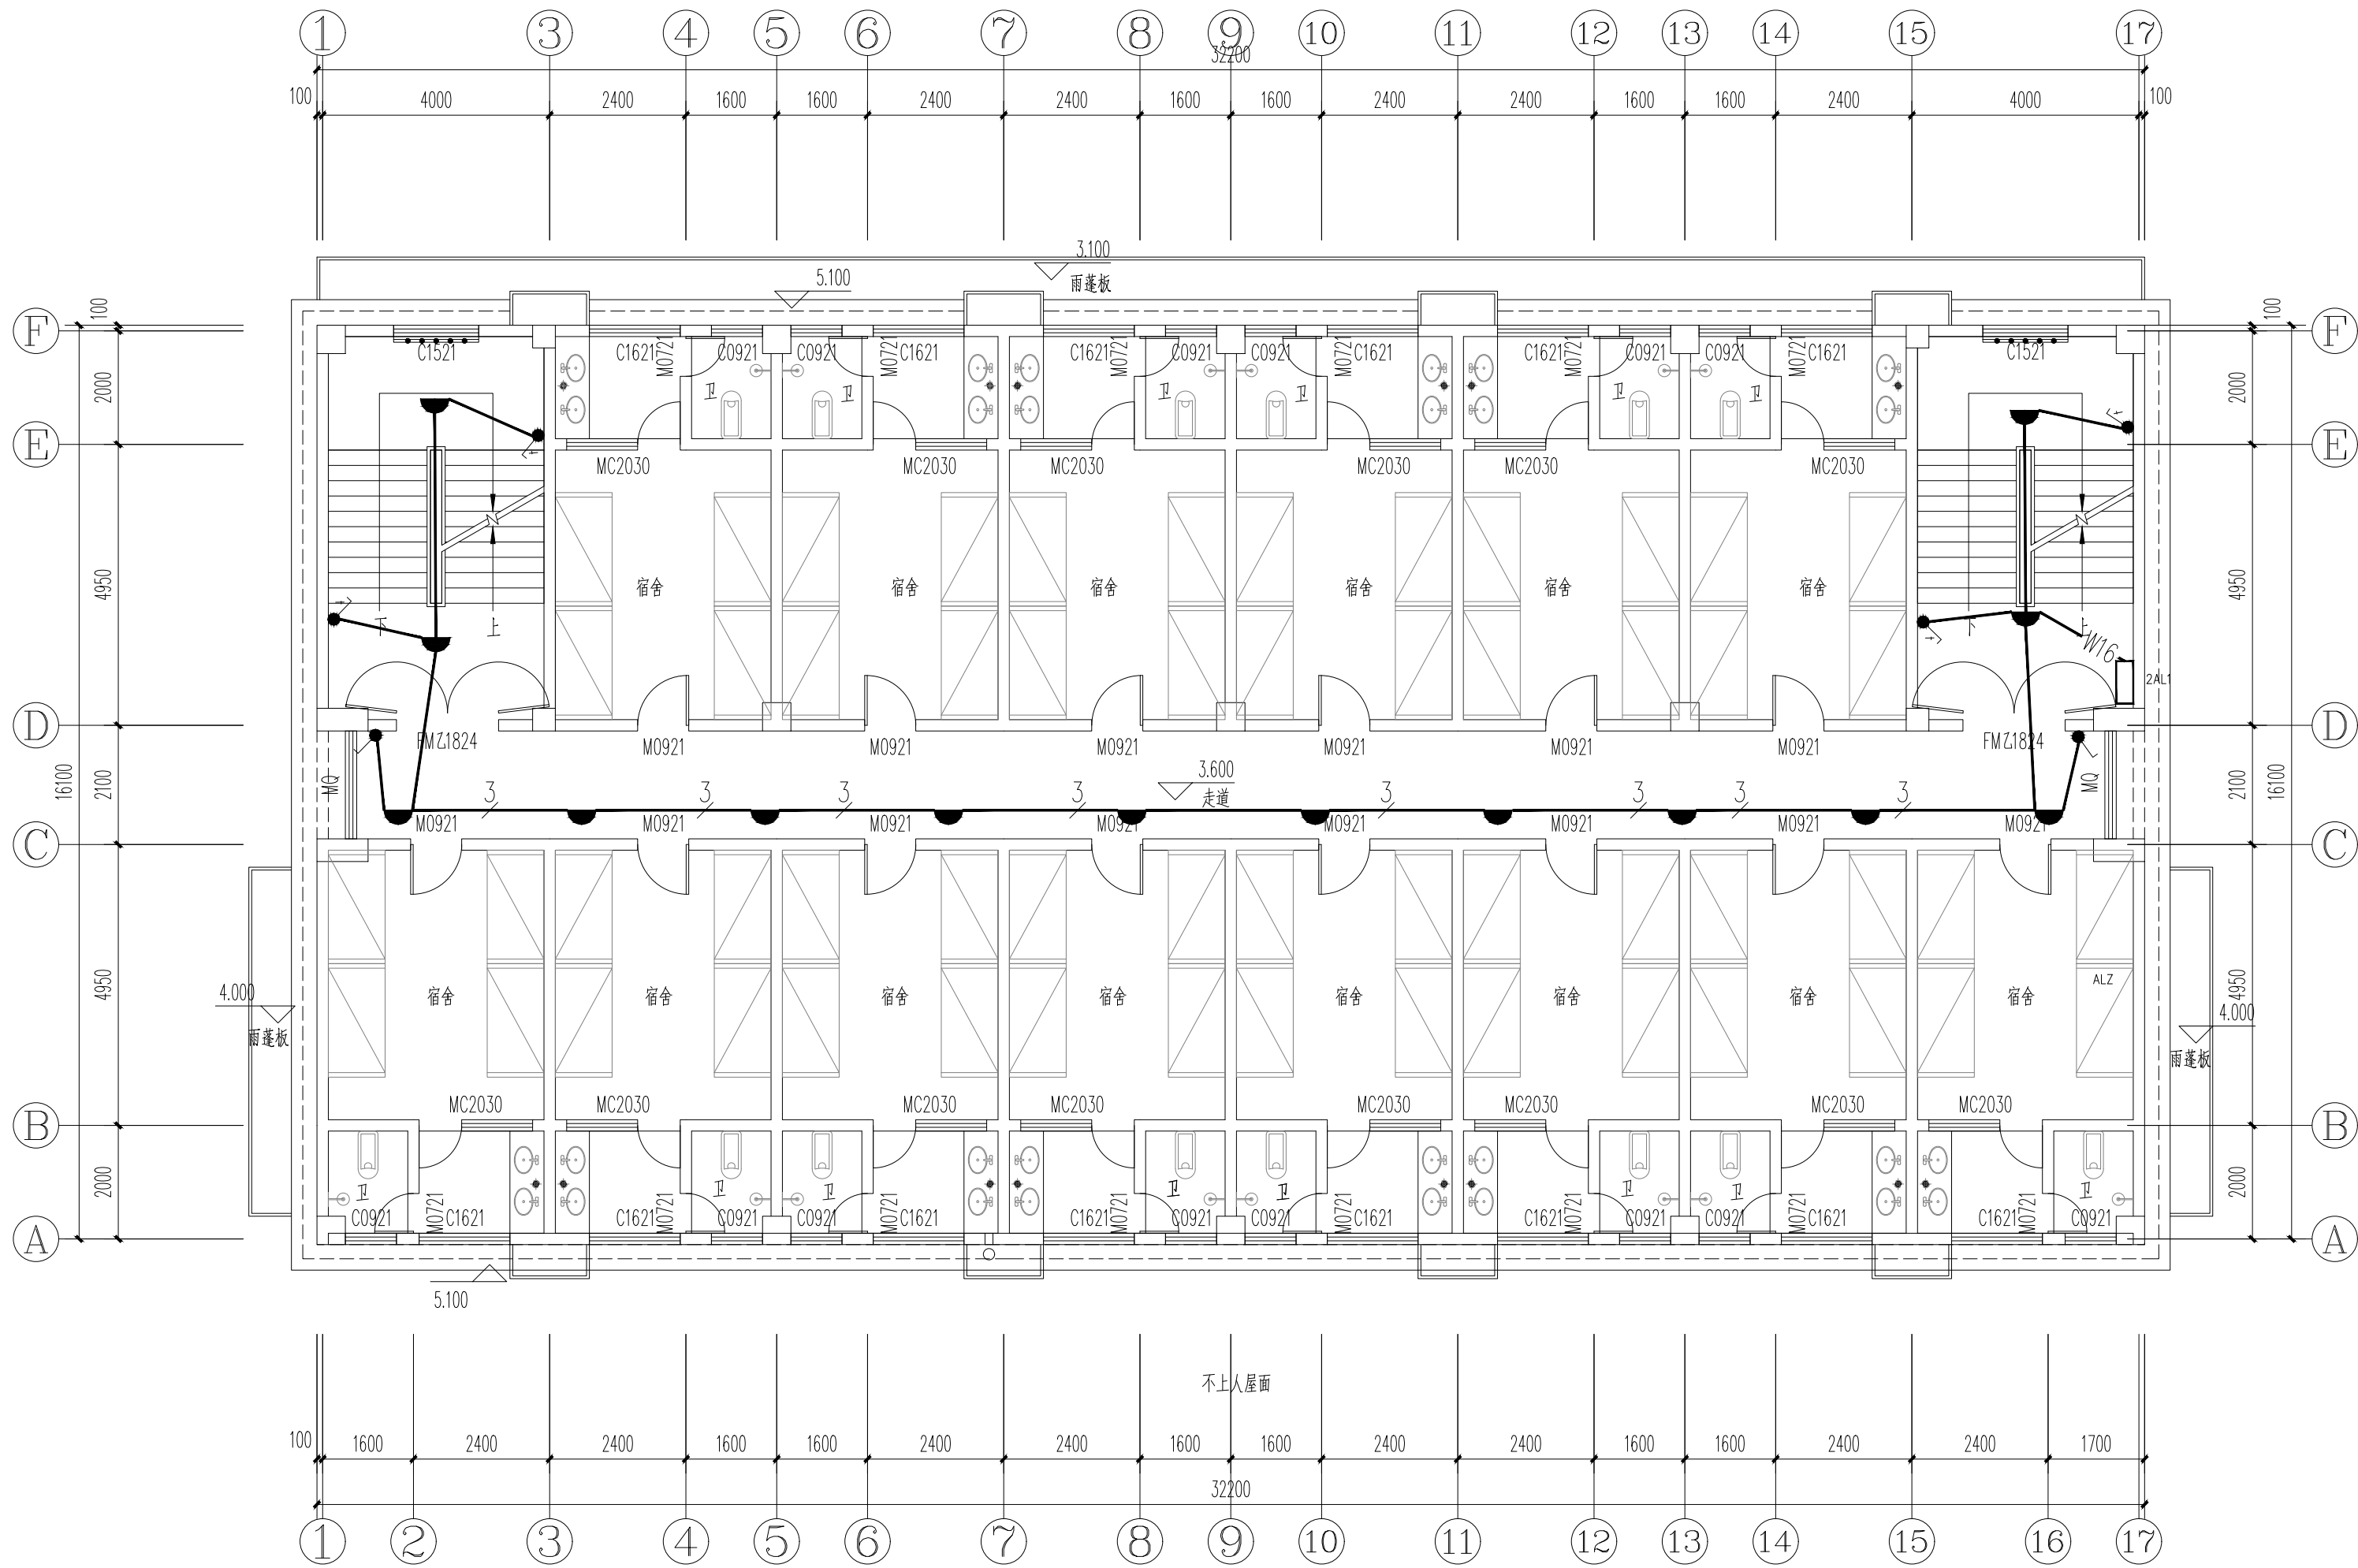

二层平面图 1:100

审定 Examined & Approved by		
审核 Examined & Verified by		
项目经理 Project Manager		
项目执行经理 Project implementation manager		
校核 Checked by		
专业负责人 Discipline Director		
设计 Designed by	赵胤臣	
会签 Confirmed by	版本号: Version No.	
建筑: ARCH	电气: ELEC	
结构: STRU	弱电: WEAK-ELEC	
给排水: WS&S	暖通: HVAC	
图别: STATUS	施工图	图号: DRAWING NO.
设计号: PROJECT NO.	42301618	日期: DATE
		2026.6



注：所有图纸以版本号数字最大者为最终版本并以此为准。

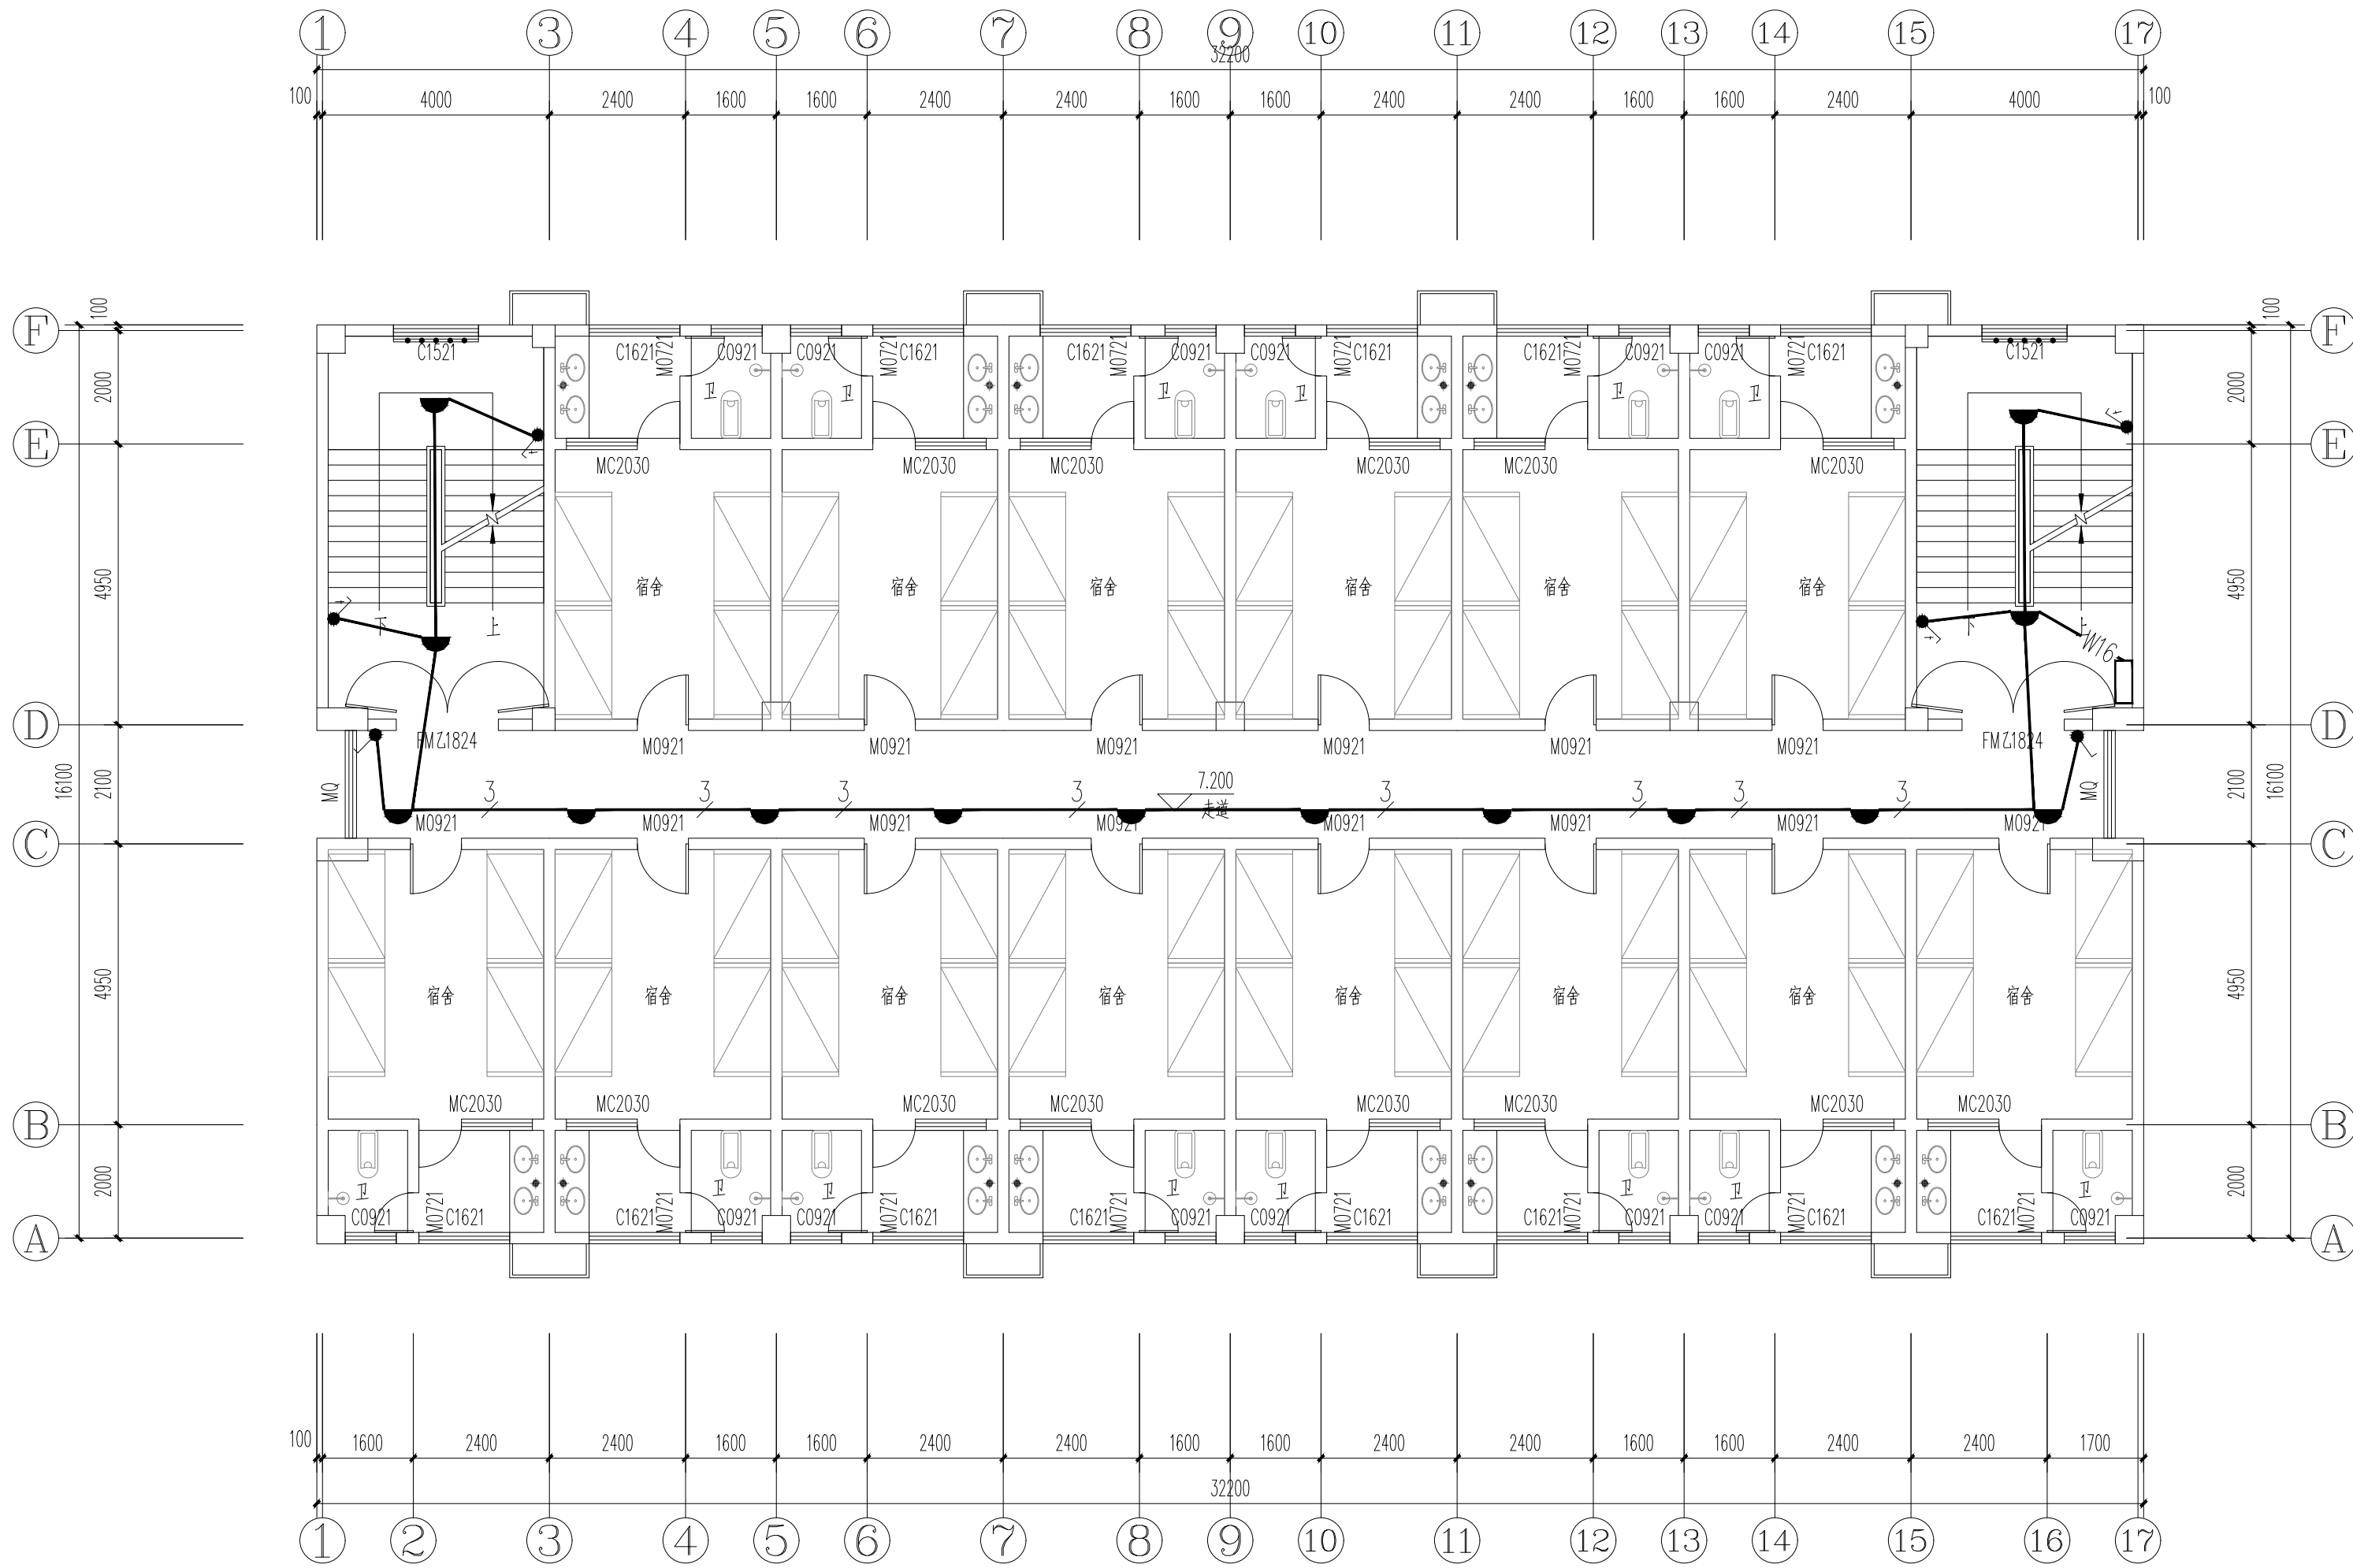

三层平面图 1:100

审定 Examined & Approved by		
审核 Examined & Verified by		
项目经理 Project Manager		
项目执行经理 Project implementation manager		
校核 Checked by		
专业负责人 Discipline Director		
设计 Designed by	赵胤臣	
会签: Confirmed by	版本号: Version No.	
建筑: ARCH	电气: ELEC	
结构: STRU	弱电: WEAK-ELEC	
给排水: WS&S	暖通: HVAC	
图别: STATUS	施工图	图号: DRAWING NO.
设计号: PROJECT NO.	42301618	日期: DATE
		2026.6


注：所有图纸以版本号数字最大者为最终版本并以此为准。

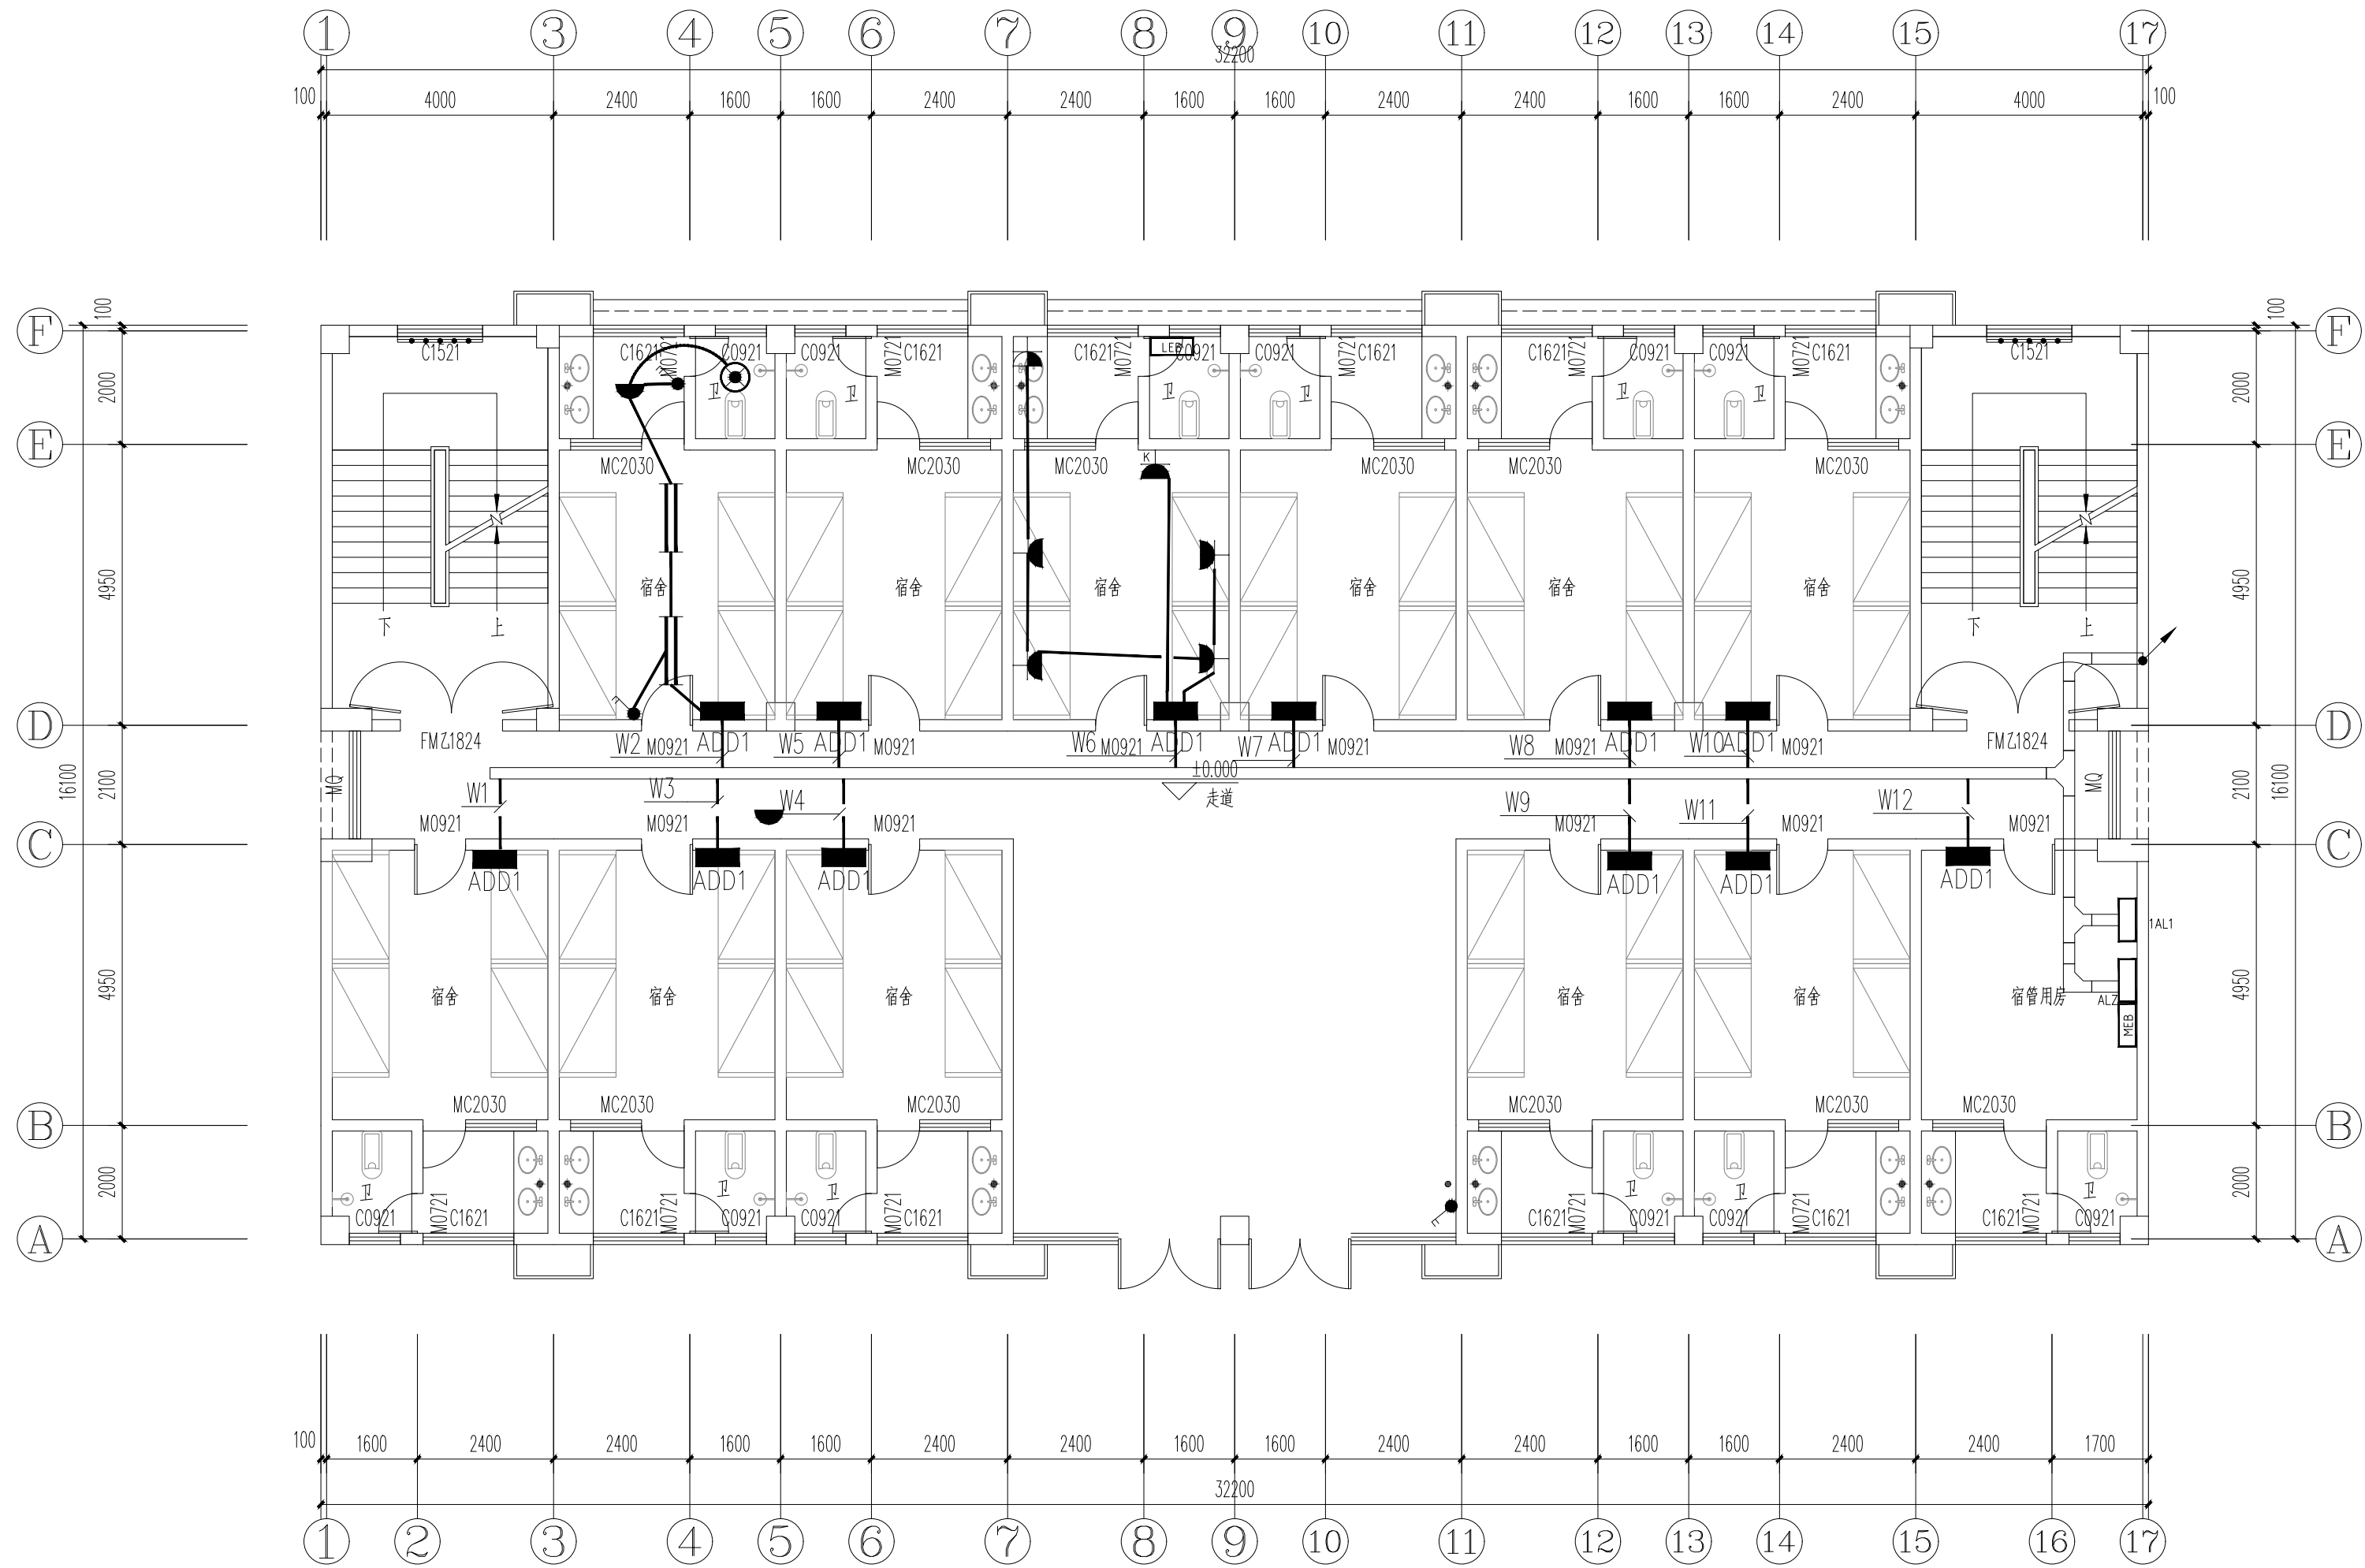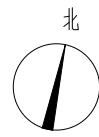


一层平面图 1:100

审定 Examined & Approved by		
审核 Examined & Verified by		
项目经理 Project Manager		
项目执行经理 Project implementation manager		
校核 Checked by		
专业负责人 Discipline Director		
设计 Designed by	赵胤臣	
会签: Confirmed by	版本号: Version No.	
建筑: ARCH	电气: ELEC	
结构: STRU	弱电: WEAK-ELEC	
给排水: WS&S	暖通: HVAC	
图别: STATUS	施工图	图号: DRAWING NO.
设计号: PROJECT NO.	42301618	日期: DATE
		2026.6

注：所有图纸以版本号数字最大者为最终版本并以此为准。

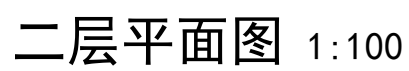


注：所有图纸以版本号数字最大者为最终版本并以此为准。

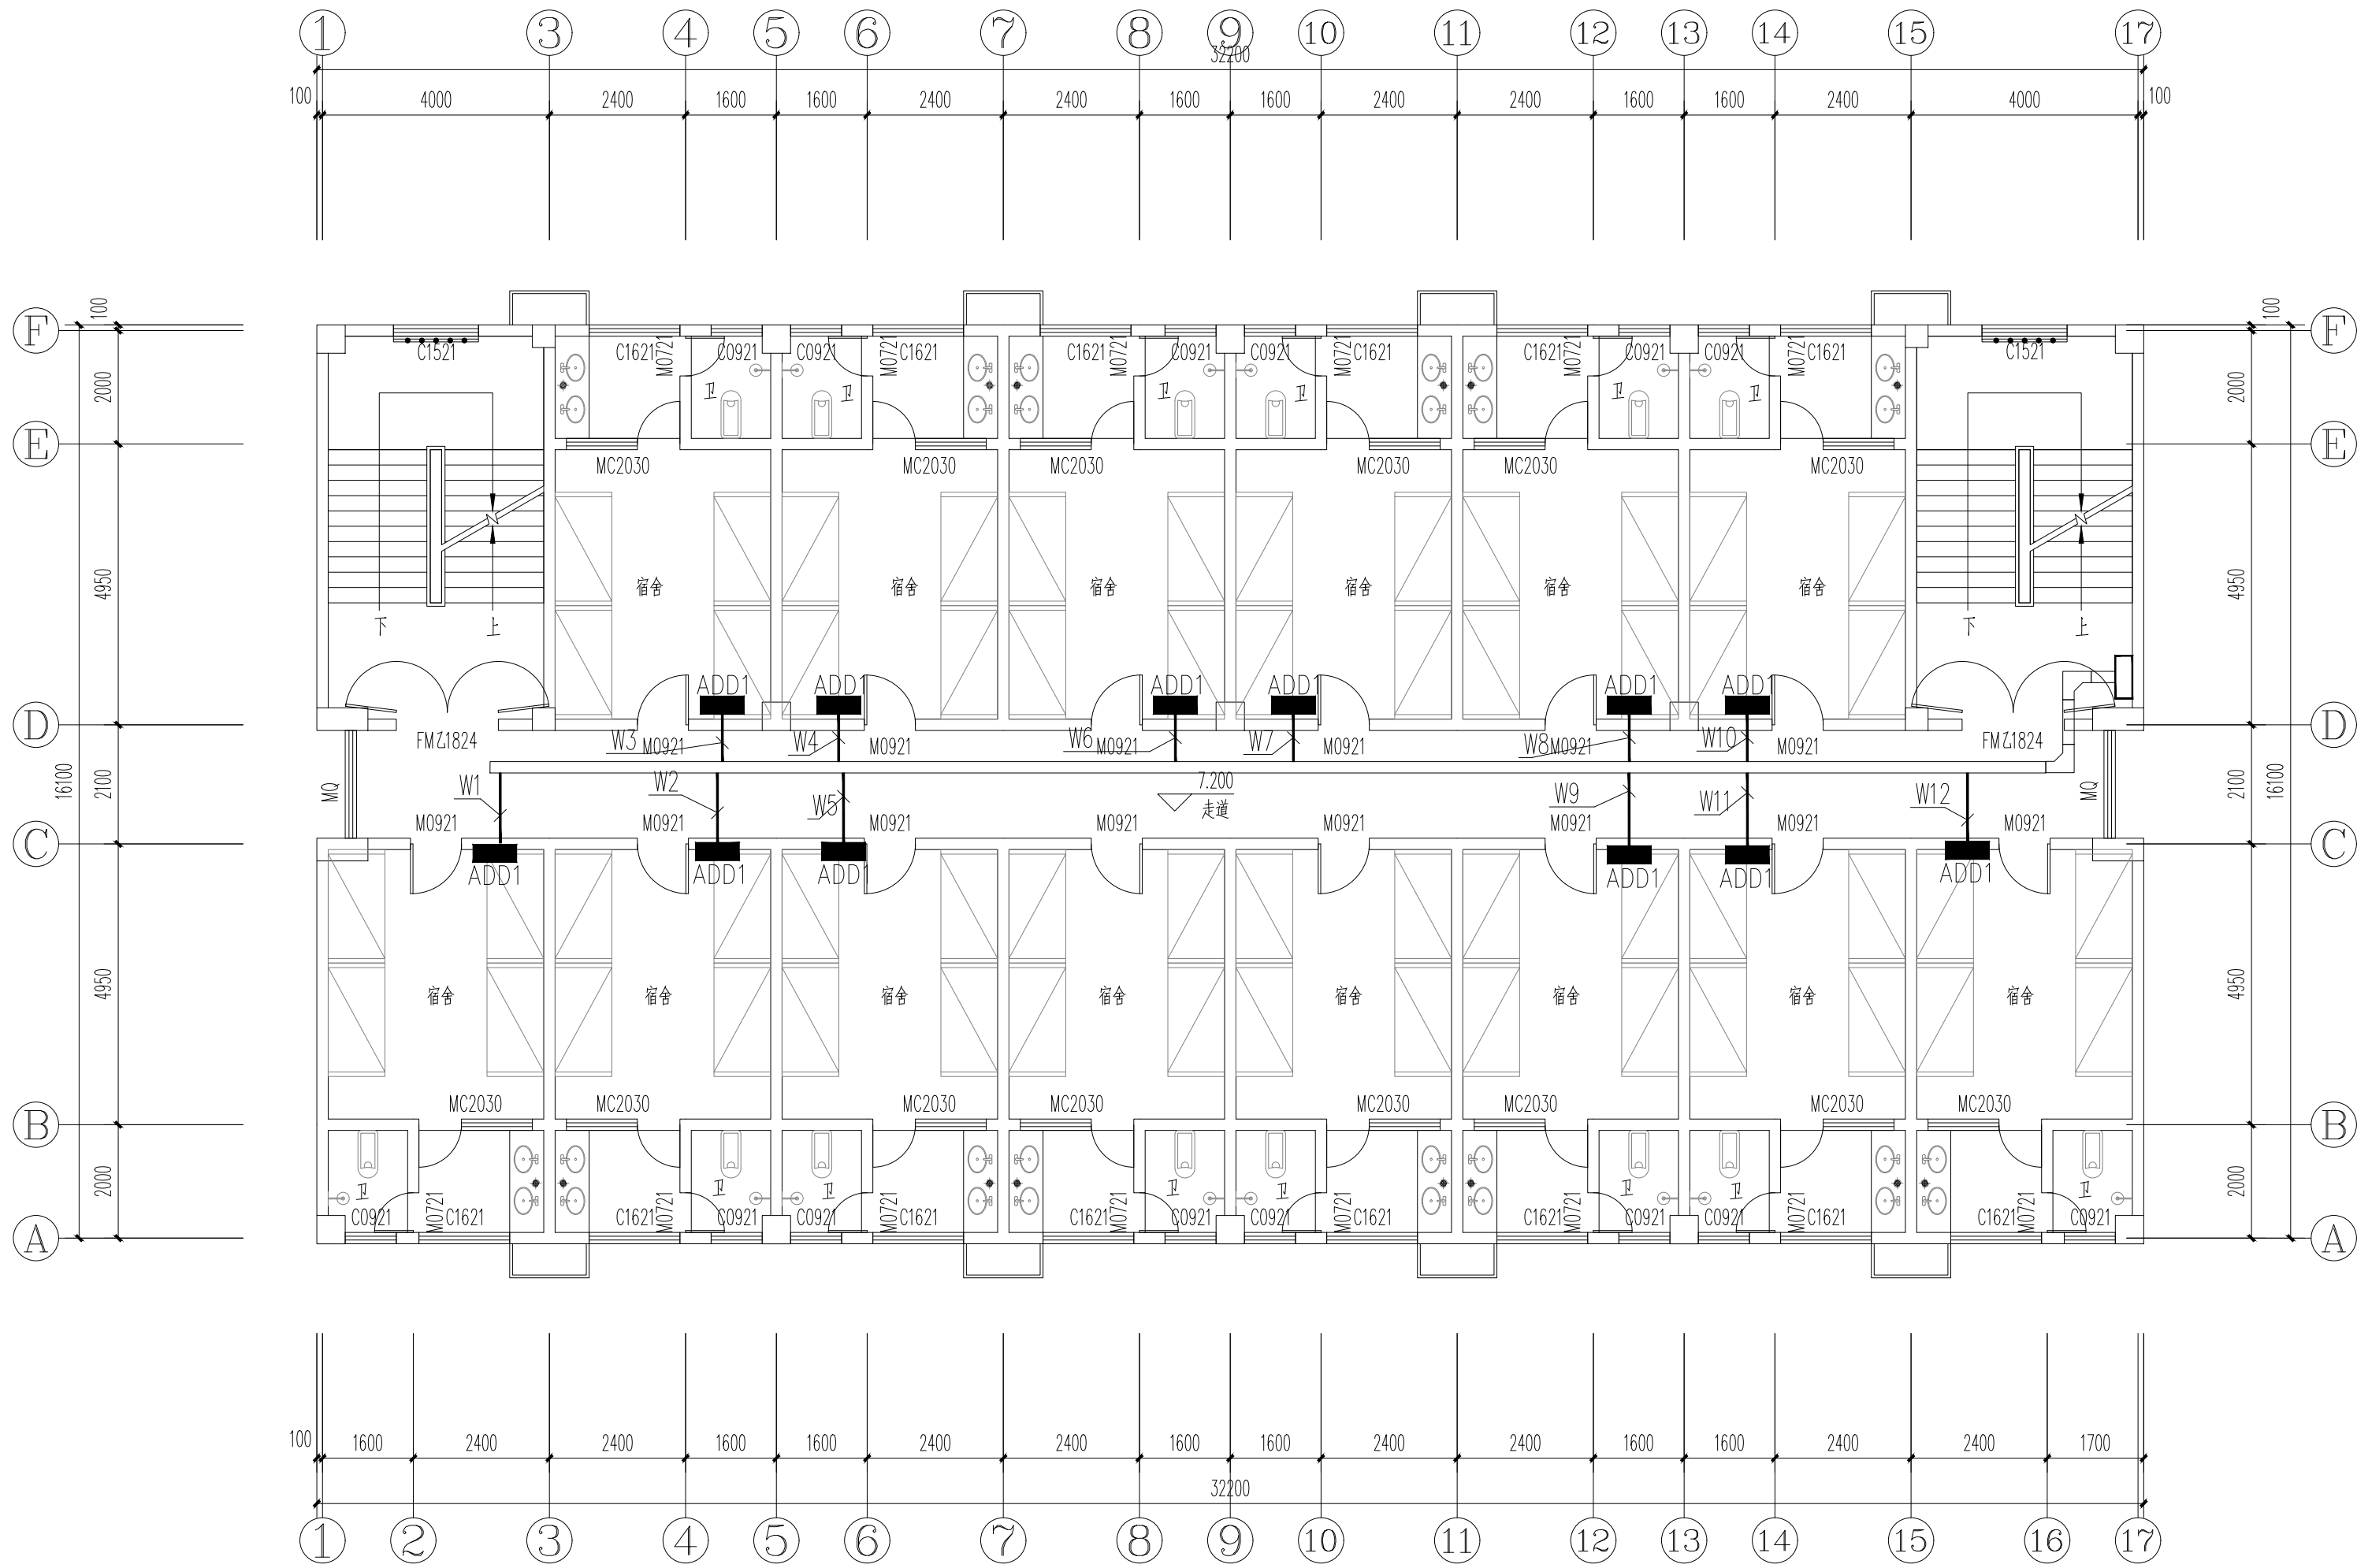

三层平面图 1:100

审定 Examined & Approved by		
审核 Examined & Verified by		
项目经理 Project Manager		
项目执行经理 Project implementation manager		
校核 Checked by		
专业负责人 Discipline Director		
设计 Designed by	赵胤臣	
会签: Confirmed by	版本号: Version No.	
建筑: ARCH	电气: ELEC	
结构: STRU	弱电: WEAK-ELEC	
给排水: WS&S	暖通: HVAC	
图别: STATUS	施工图	图号: DRAWING NO.
设计号: PROJECT NO.	42301618	日期: DATE
		2026.6

注：所有图纸以版本号数字最大者为最终版本并以此为准。

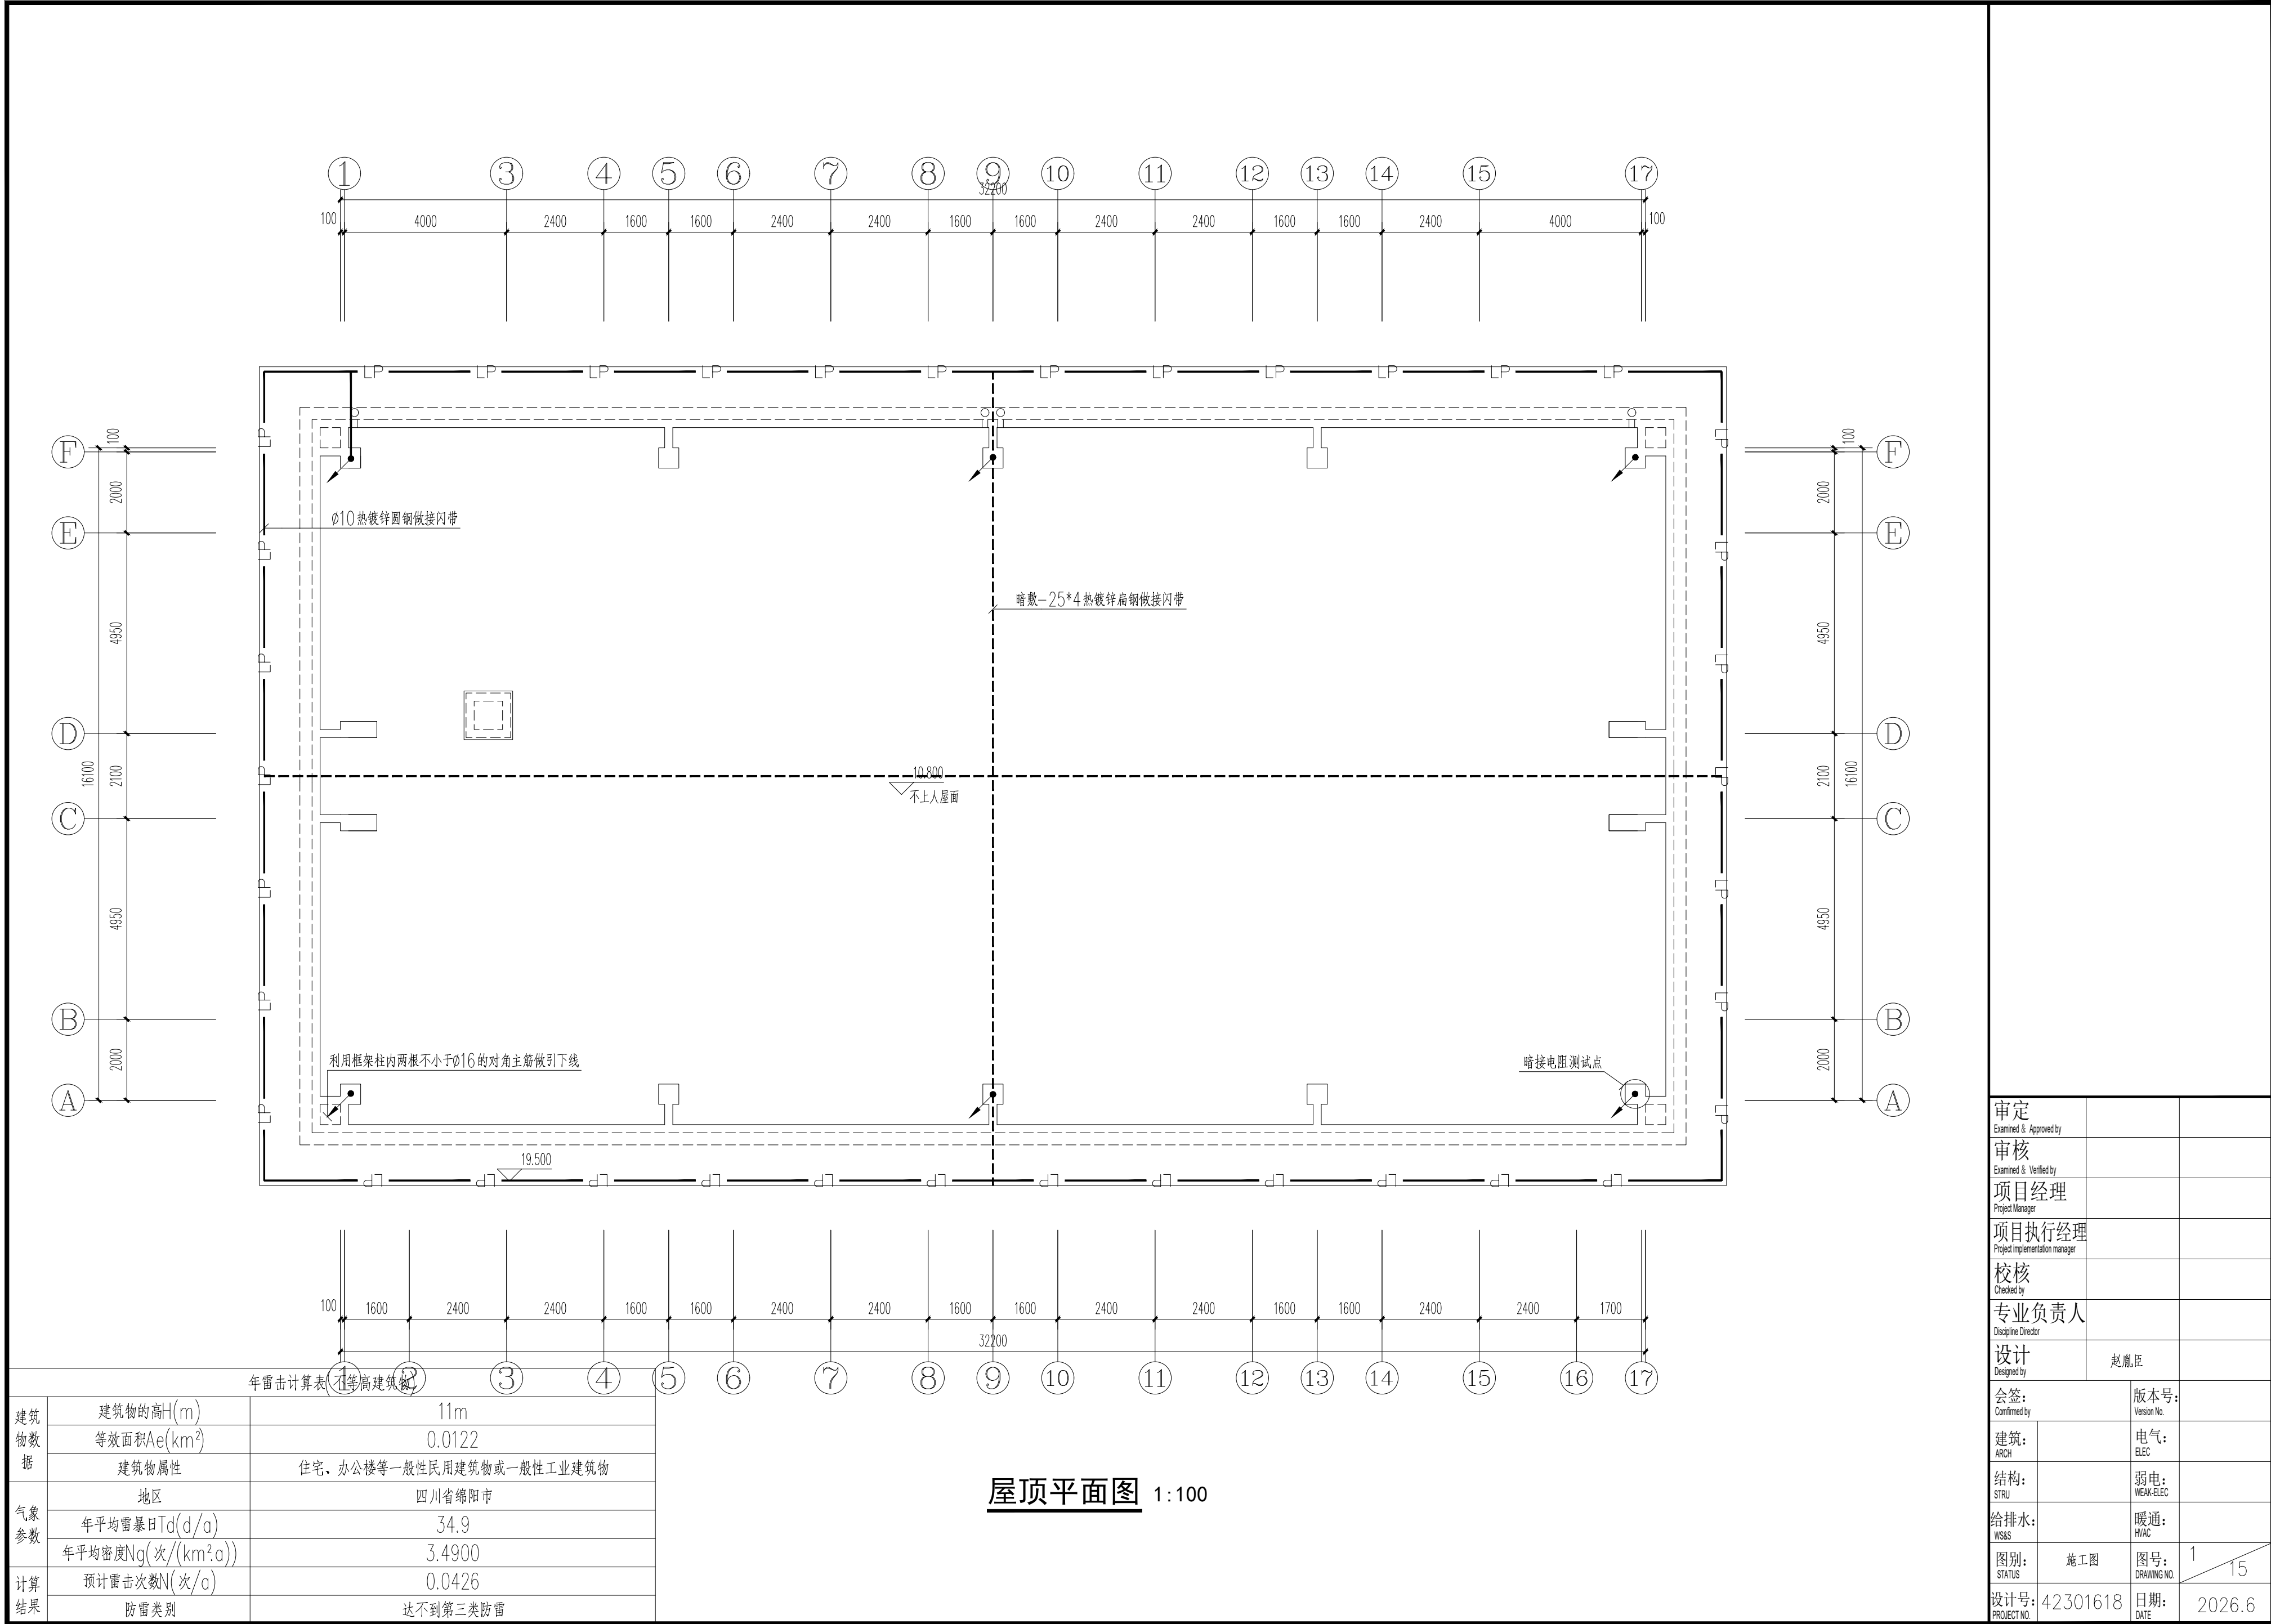


建筑 物数 据	建筑物的高H(m)	11m
	等效面积Ae(km²)	0.0122
	建筑物属性	住宅、办公楼等一般性民用建筑物或一般性工业建筑物
气象 参数	地区	四川省绵阳市
	年平均雷暴日Td(d/a)	34.9
	年平均密度Ng(次/(km².a))	3.4900
计算 结果	预计雷击次数N(次/a)	0.0426
	防雷类别	达不到第三类防雷

屋顶平面图 1:100

审定 Examined & Approved by		
审核 Examined & Verified by		
项目经理 Project Manager		
项目执行经理 Project implementation manager		
校核 Checked by		
专业负责人 Discipline Director		
设计 Designed by	赵胤臣	
会签 Confirmed by		版本号: Version No.
建筑: ARCH		电气: ELEC
结构: STRU		弱电: WEAK-ELEC
给排水: WSBS		暖通: HVAC
图别: STATUS	施工图	图号: DRAWING NO.
设计号: PROJECT NO.	42301618	日期: DATE
		2026.6

注：所有图纸以版本号数字最大者为最终版本并以此为准。


Pe=124kW,Kx=0.8,Pjs=99.2kW,Cosφ=0.85,Ijs=177.3A

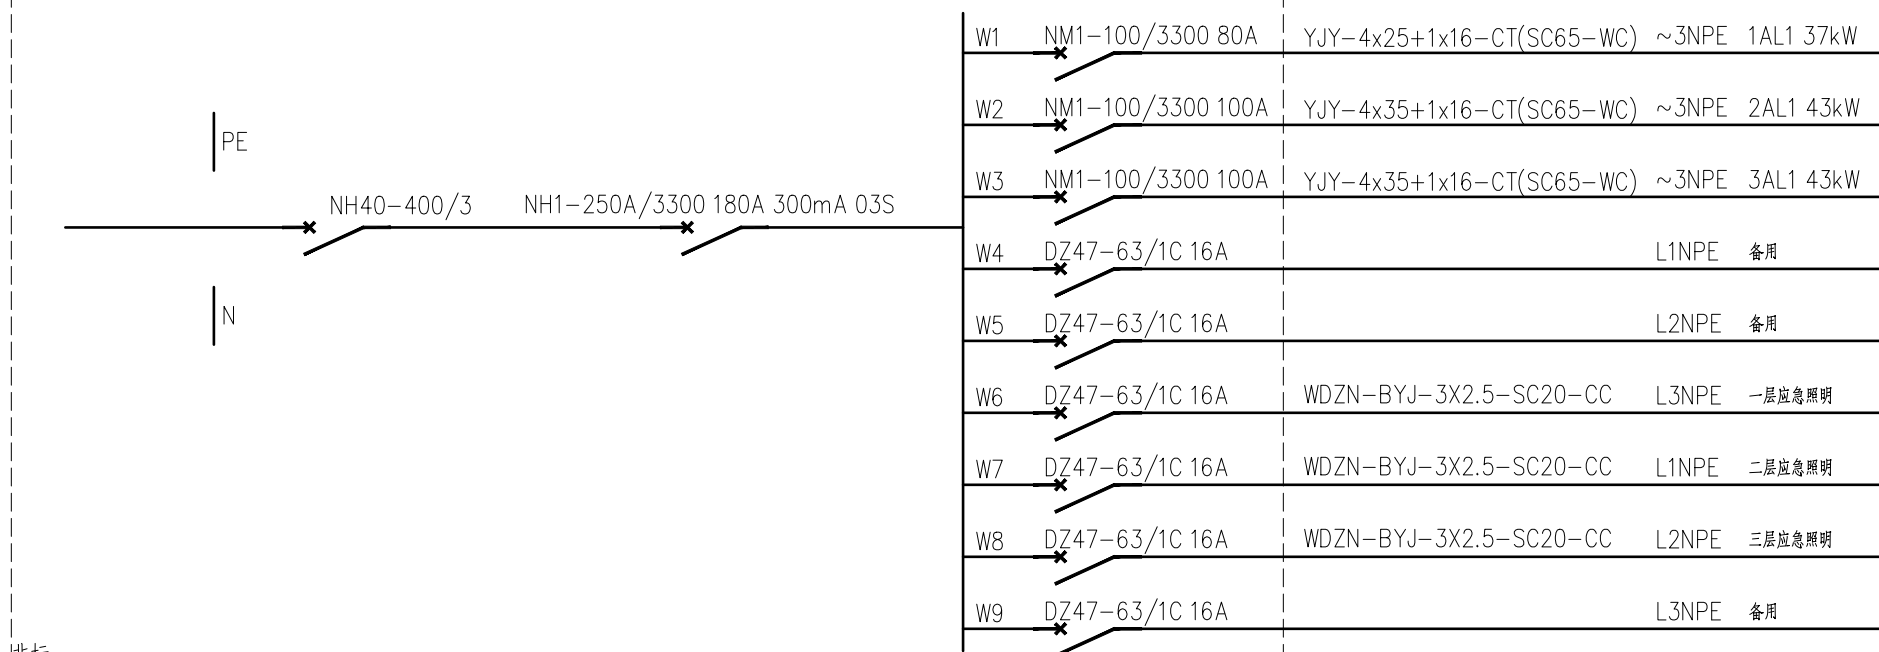

非标
距地1.6m暗装

ALZ系统图

Pe=43kW,Kx=0.8,Pjs=34.4kW,Cosφ=0.85,Ijs=61.5A

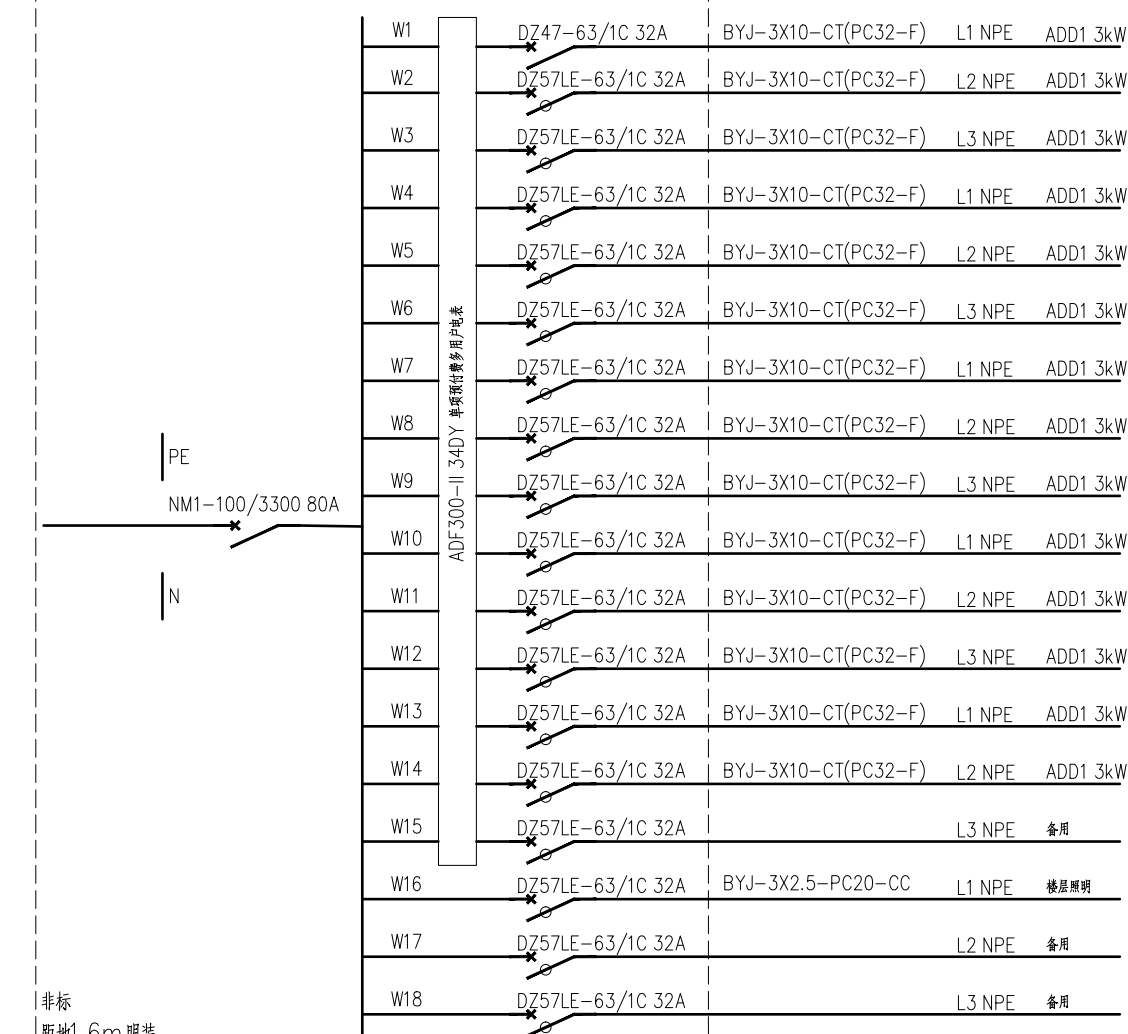


非标
距地1.6m明装

2AL1系统图


(3AL1相同)

Pe=43kW,Kx=0.8,Pjs=34.4kW,Cosφ=0.85,Ijs=63A

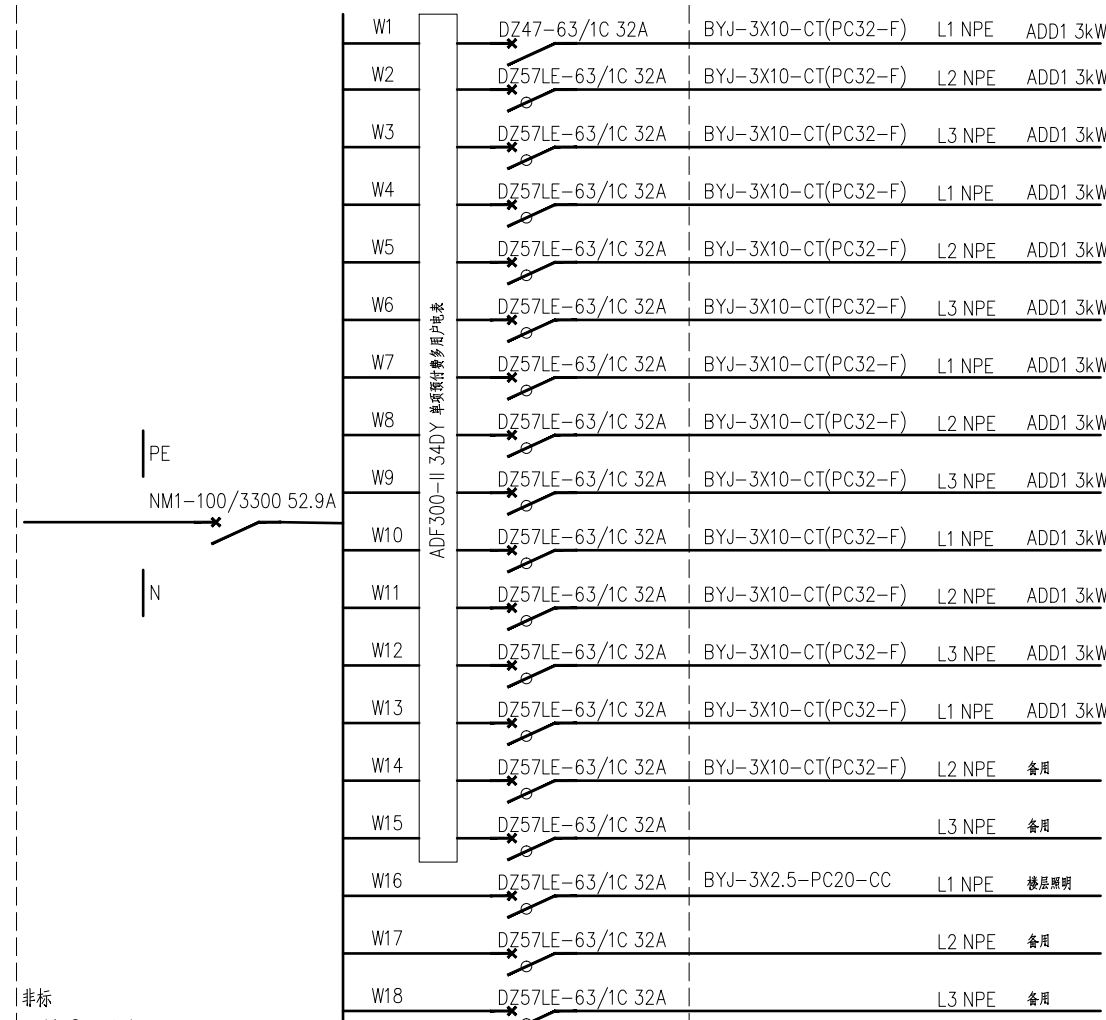

非标
距地1.6m明装


3AL1系统图

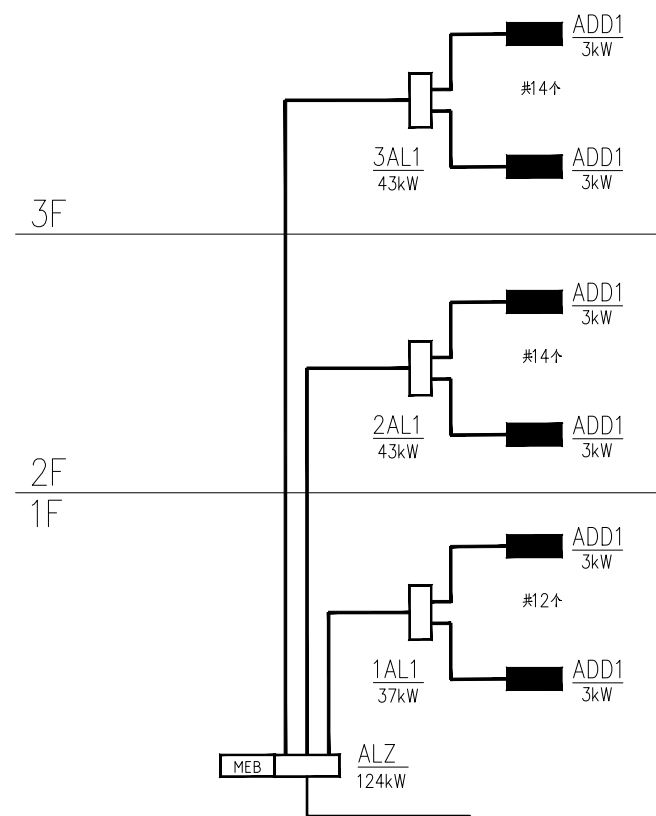


竖向配电系统图

审定 Examined & Approved by		
审核 Examined & Verified by		
项目经理 Project Manager		
项目执行经理 Project implementation manager		
校核 Checked by		
专业负责人 Discipline Director		
设计 Designed by	赵胤臣	
会签 Confirmed by	版本号: Version No.	
建筑: ARCH	电气: ELEC	
结构: STRU	弱电: WEAK-ELEC	
给排水: WS&S	暖通: HVAC	
图别: STATUS	施工图	图号: DRAWING NO.
设计号: PROJECT NO.	42301618	日期: DATE
		2026.6

注：所有图纸以版本号数字最大者为最终版本并以此为准。

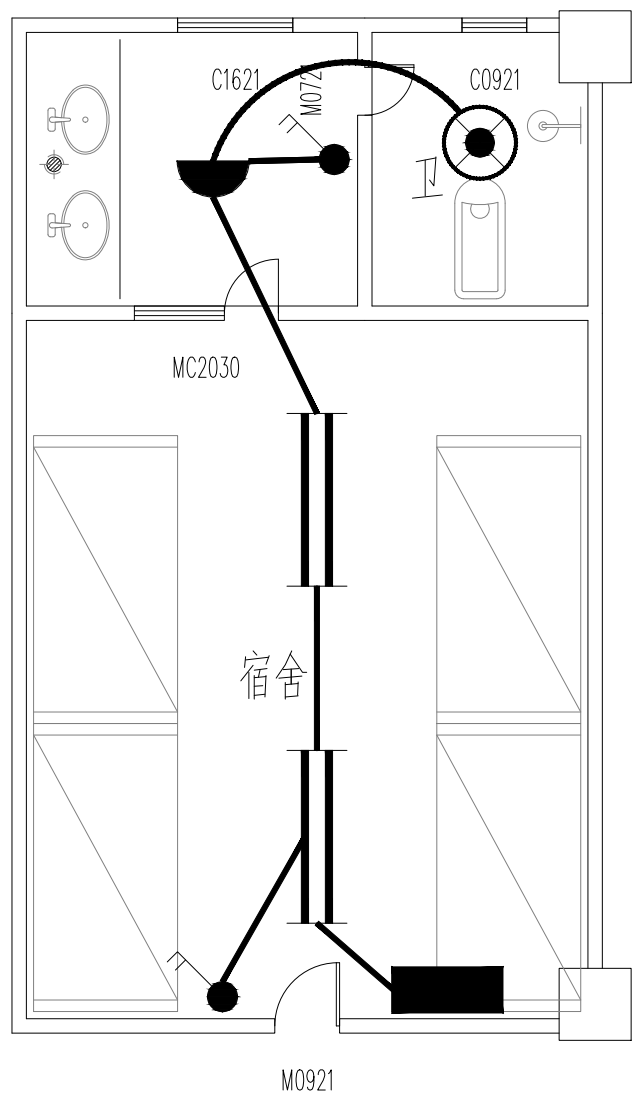


宿舍照明布置大样图

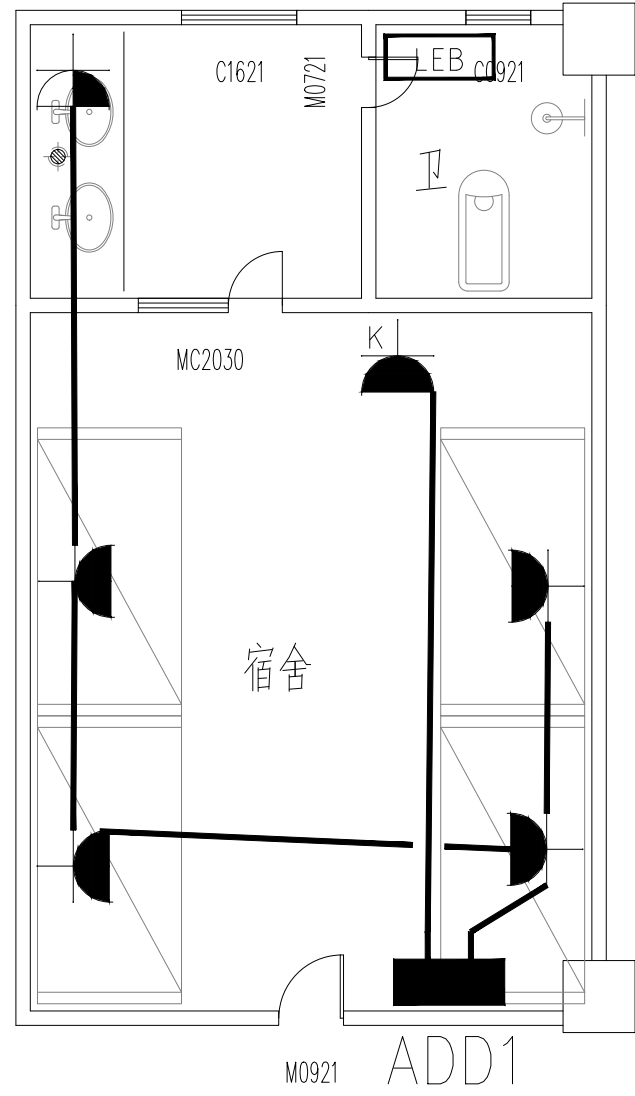

宿舍插座布置大样图

审定 Examined & Approved by		
审核 Examined & Verified by		
项目经理 Project Manager		
项目执行经理 Project implementation manager		
校核 Checked by		
专业负责人 Discipline Director		
设计 Designed by	赵胤臣	
会签: Confirmed by	版本号: Version No.	
建筑: ARCH	电气: ELEC	
结构: STRU	弱电: WEAK-ELEC	
给排水: WS&S	暖通: HVAC	
图别: STATUS	施工图	图号: DRAWING NO.
设计号: PROJECT NO.	42301618	日期: DATE
		2026.6

注：所有图纸以版本号数字最大者为最终版本并以此为准。

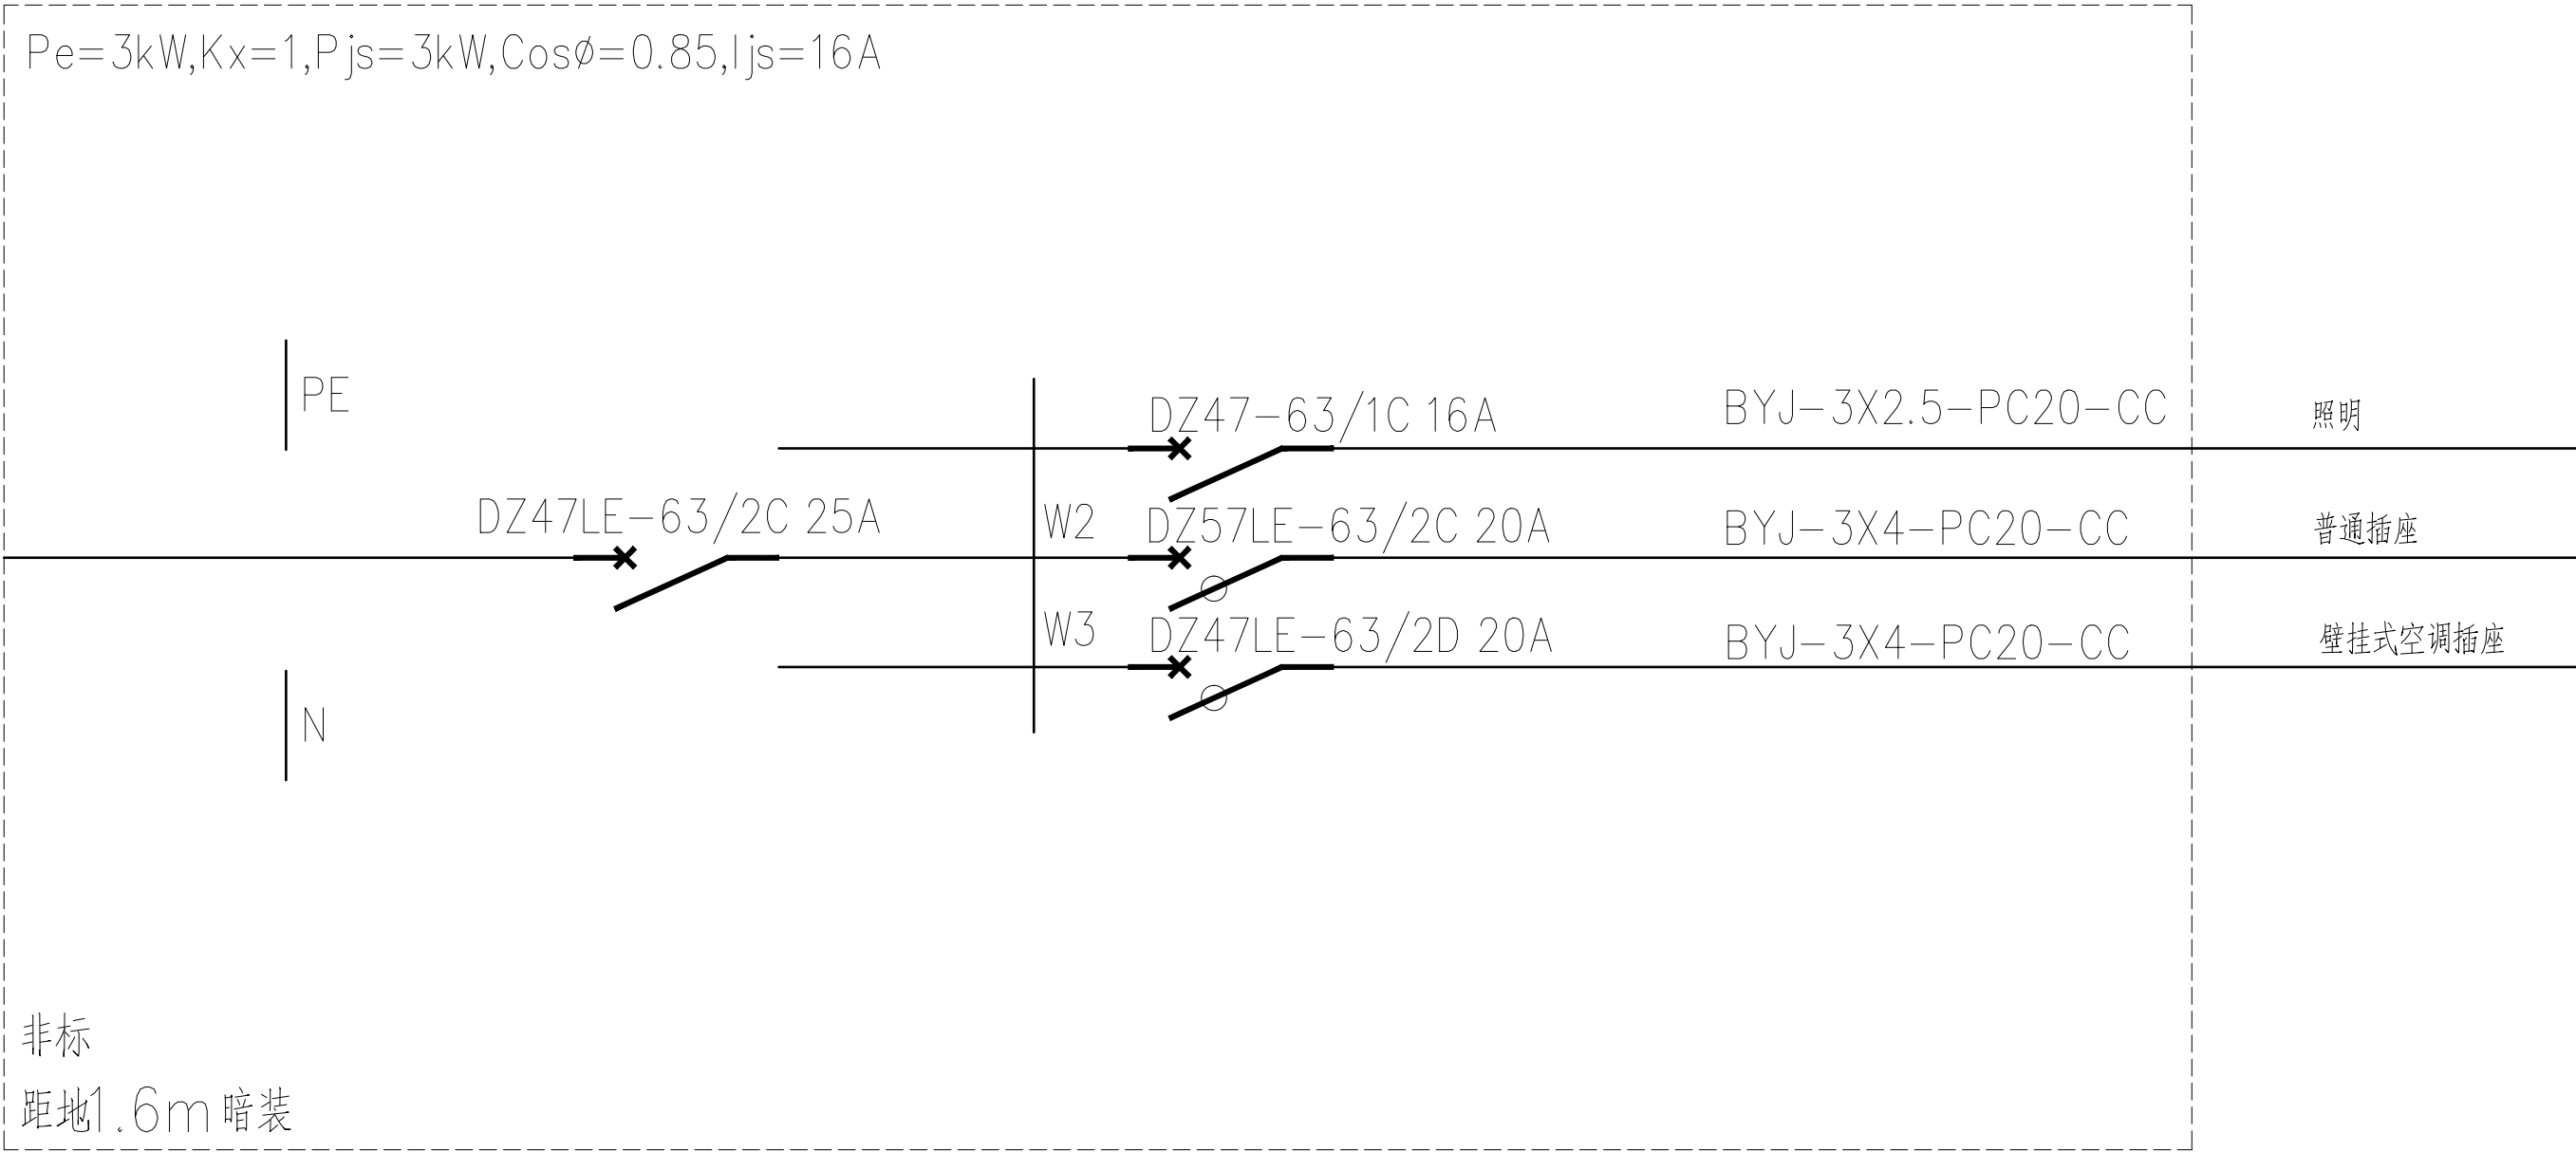

ADD1系统图

审定 Examined & Approved by		
审核 Examined & Verified by		
项目经理 Project Manager		
项目执行经理 Project implementation manager		
校核 Checked by		
专业负责人 Discipline Director		
设计 Designed by	赵胤臣	
会签: Confirmed by	版本号: Version No.	
建筑: ARCH	电气: ELEC	
结构: STRU	弱电: WEAK-ELEC	
给排水: WS&S	暖通: HVAC	
图别: STATUS	施工图	图号: DRAWING NO.
设计号: PROJECT NO.	42301618	日期: DATE
		1 15 2026.6

注：所有图纸以版本号数字最大者为最终版本并以此为准。

序号	图例	名称	规格	单位	数量	备注
1		屏、台、箱、柜		台	10	
2		局部等电位端子箱		台	2	
3		总等电位端子箱		台	2	
4		照明配电箱		台	36	
5		自带电源疏散照明灯(A型)		盏	11	
6		方向标志灯(右向)		盏	8	
7		方向标志灯(双向)		盏	2	
8		方向标志灯(左向)		盏	10	
9		集中电源疏散照明灯(B型)——壁装型		盏	12	
10		楼层标志灯		盏	4	
11		安全出口标志灯		盏	6	
12		疏散出口标志灯		盏	2	
13		天棚灯	30W	盏	41	
14		双管荧光灯	2x36W	盏	2	
15		防水防尘灯		盏	1	
16		空调插座		个	1	
17		带保护接点暗装插座		个	4	
18		带保护接点防爆插座		个	1	
19		开关		个	13	
20		延迟开关		个	6	
21		双联开关		个	3	
22		BV导线	BV,2.5	米	935.4	(结果不含垂直长度)
23		引线		个	5	
24				米	6.2	(结果不含垂直长度)
25		穿低压流体输送用焊接钢管(钢管)敷设 SC15		米	311.8	(结果不含垂直长度)
26		桥架	200 X 100	米	108.2	槽式直通桥架
27		弯通	200X100	件	10.0	槽式水平等径弯通

配电系统设计说明

一、设计依据

本设计遵照现行国家规范：《民用建筑电气设计标准》GB 51348、《建筑物防雷设计规范》GB50057、《低压配电设计规范》GB50054、《建筑照明设计标准》GB50034；同时依据本项目建筑专业平立面施工图、建设方供电主管部门批复意见及现场勘测资料开展设计。

二、配电系统负荷计算（微调参数 + 补充说明）

1. 负荷参数

设备额定总功率

Pe=126kW

，需要系数

K x =0.8计算负荷P js=99.2kW功率因数cosφ=0.85计算电流js=177.3A

增补：本项目负荷按三级民用建筑负荷设计，无一级 / 二级消防重要负荷，普通动力 + 照明混合配电，后期增设大功率设备需复核变压器及开关容量。

2. 配电箱配置

单体配电末端共 18 个 W1~W18 配电支路，分普通用电回路与备用回路；

配电总箱设置：1AL1、2AL1、3AL1 总配电柜，进线总开关选用 NM1-100/3300 塑壳断路器（额定电流 80A/100A 二档可选）；支路断路器统一采用 DZ47-63 系列微型断路器，整定电流分 16A、32A 两种规格。

删减：去除原文冗余表述，补充：所有断路器带短路 + 过载保护，照明支路增设漏电可选配置。

三、线缆选型及敷设（优化敷设描述，增补防火要求）

主干进线电缆：YJY-5×35、YJY-5×75 铜芯电力电缆，配电柜内设 CT 电流互感器 + SC 焊接钢管防护敷设；

室内分支线缆：

普通配电：BYJ-3×10 绝缘电线；

应急配电：WDZN-BYJ-3×25 低烟无卤耐火线缆，穿 PC32、PC20 阻燃塑料管暗敷；

增补：所有阻燃线缆满足 GB/T19666 阻燃标准，FC 地面暗敷、CC 顶板暗敷严格区分敷设场景；

配电制式：三相五线制

L1/L2/L3+N+PE

，PE 线单独接地保护，插座回路、照明回路分路独立设置漏电保护（新增：插座回路漏电动作电流 30mA，照明回路按需选配）。

四、照明与插座配电（细化分区，增补应急照明）

各功能区域按使用属性分区设置动力、普通照明、应急照明回路，各房间配电箱就地分路控制，单回路额定功率控制≤3kW；

普通照明：常规单相配电回路；

应急照明：独立专用配电回路，线缆统一采用 WDZN-BYJ 耐火电线单独配电；

新增：疏散应急照明灯具自带蓄电池，断电后持续点亮≥90min，满足消防疏散规范。

五、防雷接地设计（优化参数 + 增补接地做法）

项目地处四川绵阳，年雷暴日 T d =34.9d 年预计雷击次数，建筑等效面积A e=0.0122km 平方，

按第三类防雷建筑物设计；

屋面预留防雷测试点位，屋面采用屋面避雷带沿檐口敷设，屋面金属构配件、设备外壳全部就近与避雷引下线可靠连通；

增补接地系统：本工程采用总等电位 MEB + 局部等电位 LEB 联结，配电 PE 干线、给排水金属管道、强弱电桥架统一接入等电位端子；PE 线全程不允许断线、不串接设备。

六、施工说明（精简原文序号，增补施工管控要求）

所有线缆敷设、开关选型、敷设方式严格遵照系统图、平面图纸施工，线路走向参照建筑一~三层弱电平面图纸（原序号②③④⑥⑦⑧⑩~⑪整合精简）；

PE 保护线全程连续贯通，严禁断线、串接、私自外接；箱体金属外壳、落地配电箱柜体必须可靠接 PE 保护；

审定 Examined & Approved by		
审核 Examined & Verified by		
项目经理 Project Manager		
项目执行经理 Project implementation manager		
校核 Checked by		
专业负责人 Discipline Director		
设计 Designed by	赵胤臣	
会签： Confirmed by	版本号： Version No.	
建筑： ARCH	电气： ELEC	
结构： STRU	弱电： WEAK-ELEC	
给排水： WSBS	暖通： HVAC	
图别： STATUS	施工图	图号： DRAWING NO.
设计号： PROJECT NO.	42301618	日期： DATE
		2026.6

注：所有图纸以版本号数字最大者为最终版本并以此为准。

图纸目录					
	序号	图 纸 名 称	图号	规格	版次号
	1	一层建筑平面图	ARCH-01	A2	A
	2	二层建筑平面图	ARCH-02	A1	A
	3	三层建筑平面图	ARCH-03	A1	A
	4	屋顶平面图	ARCH-04	A1	A
	5	1AL1 配电系统图	ELEC-01	A1	A
	6	2AL1 配电系统图	ELEC-02	A1	A
	7	3AL1 配电系统图	ELEC-03	A1	A
	8	宿舍照明布置大样图	ELEC-04	A1	A
	9	宿舍插座布置大样图	ELEC-05	A1	A

审定 Examined & Approved by		
审核 Examined & Verified by		
项目经理 Project Manager		
项目执行经理 Project implementation manager		
校核 Checked by		
专业负责人 Discipline Director		
设计 Designed by	赵胤臣	
会签: Confirmed by		版本号: Version No.
建筑: ARCH		电气: ELEC
结构: STRU		弱电: WEAK-ELEC
给排水: WS&S		暖通: HVAC
图别: STATUS	施工图	图号: DRAWING NO.
设计号: PROJECT NO.	42301618	日期: DATE
		1 15 2026.6

注：所有图纸以版本号数字最大者为最终版本并以此为准。